


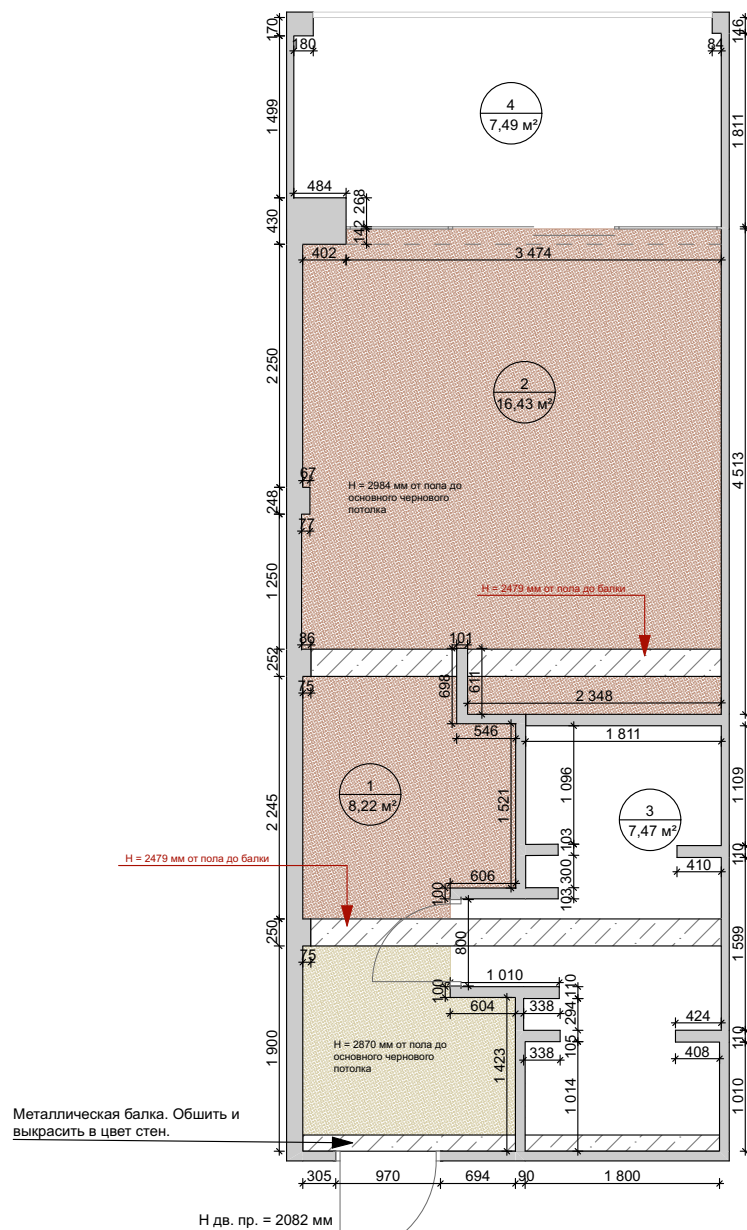

№	Наименование	Площадь
1	Прихожая	8,22
2	Зона спальни	16,43
3	Санузел	7,47
4	Балкон	7,49
		39,61 м²

- 1) Уточнить размещение кондиционеров, их управление (с пульта, или панель на стене).
- 2) Уточнить открывание дверей.
- 3) Обмерный план выполнен по обмерам сторонней организации и может не учитывать все особенности помещения и иметь размеры, отличающиеся от реальных.
- 4) Перед началом строительных работ все размеры необходимо уточнить на месте.
- 5) Все размеры указаны без учета отделочных материалов.
- 6) Если натяжной потолок будет установлен ниже уровня потолочных балок, то размещение потолочных светильников нужно изменить. Согласовать с дизайнером и заказчиками.

-  - зона чернового потолка
-  - зона чернового потолка
-  - балка
-  - влагостойкий белый матовый натяжной потолок.
-  - светодиодная лента
-  - подвесной светильник в санузле - 2 шт
-  - встроенный потолочный светильник в санузле - 3 шт
-  - встроенный потолочный светильник в санузле в душевой- 1 шт
-  - встроенный потолочный светильник в прихожей - 3 шт
-  - встроенный потолочный светильник в зоне спальни - 5 шт
-  - подвесной потолочный светильник у кровати в зоне спальни - 2 шт

Изм.	Копуч.	Лист	№Док.	Подп.	Дата				
						Room 381	Стадия	Лист	Листов
						План потолка. М1:70			