


№	Наименование	Площадь
1	Прихожая	8,22
2	Зона спальни	16,43
3	Санузел	7,47
4	Балкон	7,49
		39,61 м²

Примечания:

Обязательно перепроверить размеры помещения, тк могут быть расхождения с обмерным планом!!!

- 1)Уточнить размещение кондиционеров, их управление (с пульта, или панель на стене).
- 2) Уточнить какой замок при входе в номер, и где размещать.
- 3)Обмерный план выполнен по обмерам сторонней организации и может не учитывать все особенности помещения и иметь размеры, отличающиеся от реальных.
- 4) Перед началом строительных работ все размеры необходимо уточнить на месте.
- 5) Все размеры указаны без учета отделочных материалов.
- 6) Сантехническое оборудование в санузле находится на прежних местах.
- 7) Сантехническое оборудование которое пригодно к эксплуатации не подлежит замене.
- 8) Глубина кухонного гарнитура если технически возможно может остаться 546 мм, если технически должна быть стандартного размера 600 мм, то нужно нарастить стену вдоль гарнитура на 54 мм. Согласовать с строителями и проектировщиками кухонного гарнитура.

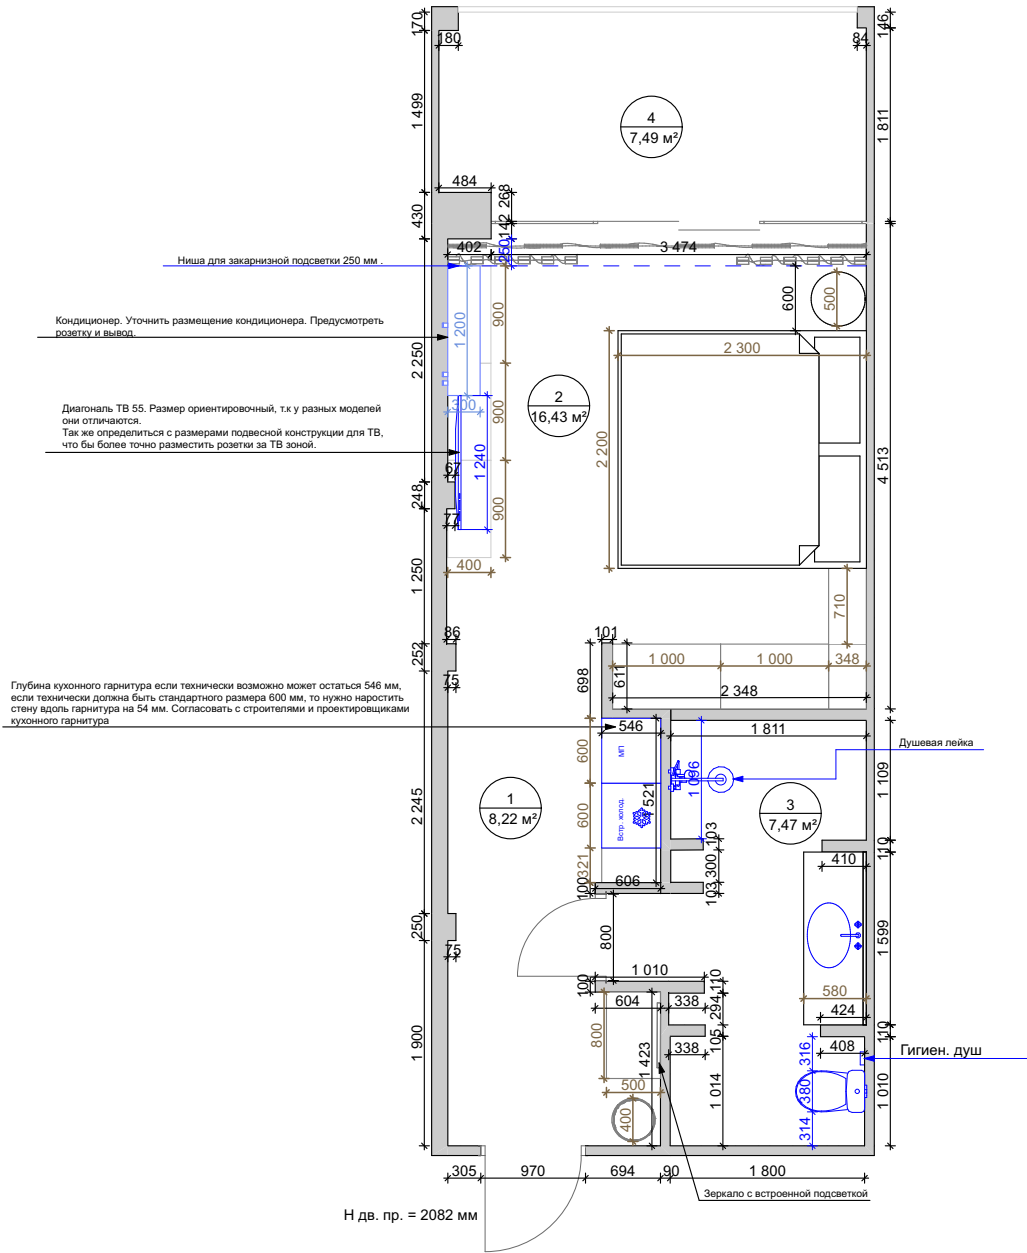

Изм.	Копуч.	Лист	№Док.	Подп.	Дата				
						Room 381	Стадия	Лист	Листов
						План размещения сантехнического и электрооборудования. М1:70			