№	Наименование	Площадь
1	Прихожая	8,22
2	Зона спальни	16,43
3	Санузел	7,47
4	Балкон	7,49
		39,61 м²

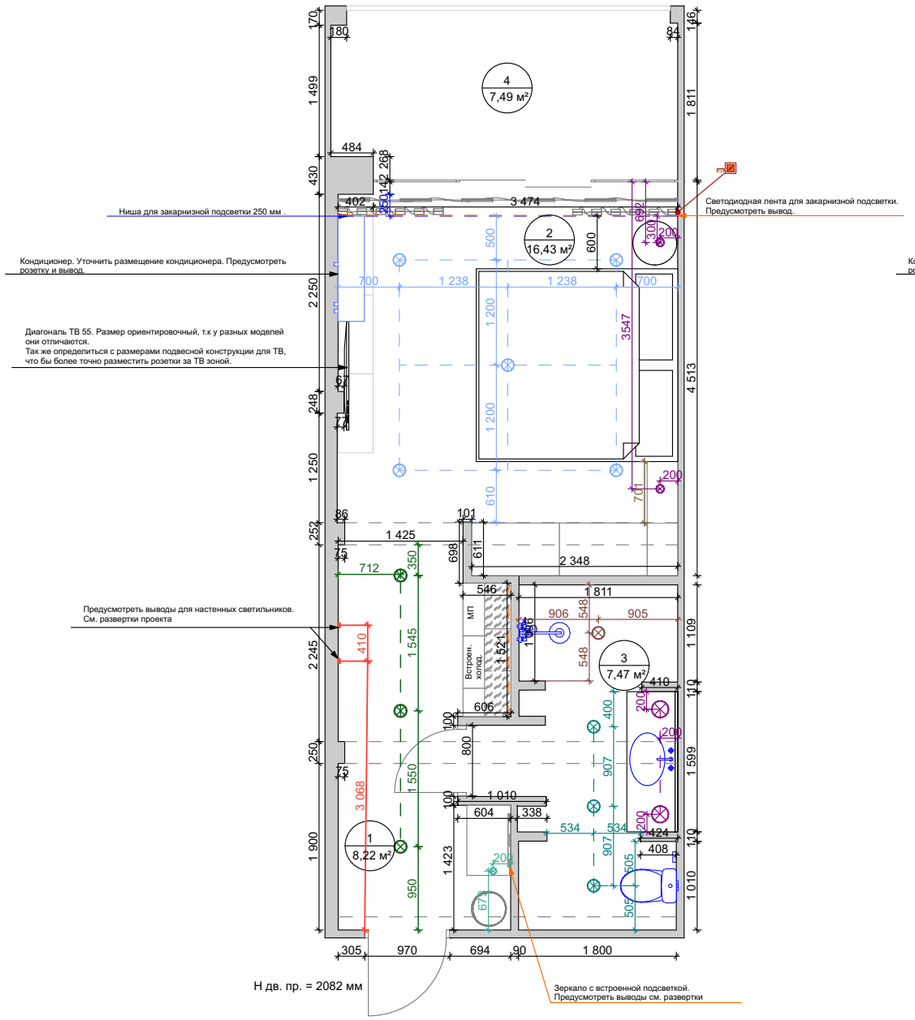

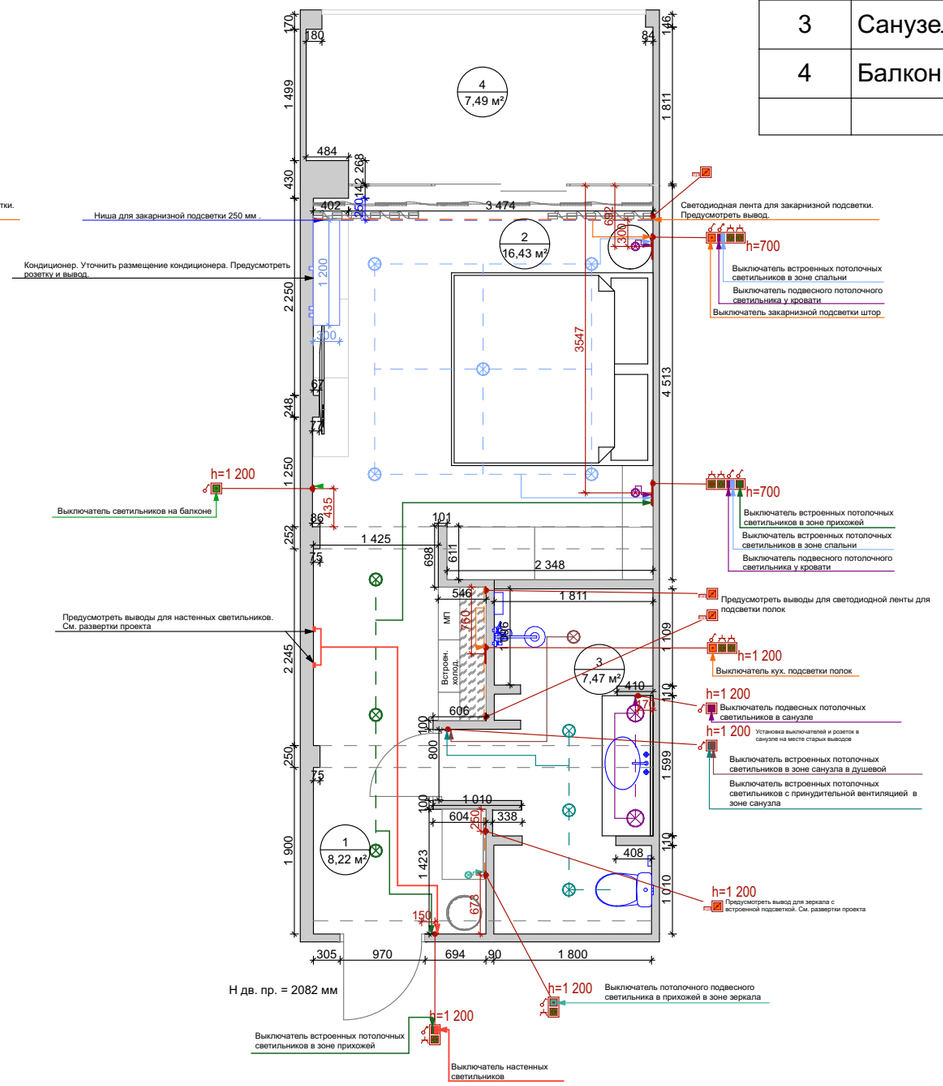

Примечания:

Обязательно перепроверить размеры помещения, тк могут быть расхождения с обмерным планом!!!

1)Уточнить размещение кондиционеров, их управление (с пульта, или панель на стене).
2) Уточнить какой замок при входе в номер, и где размещать.
3)Обмерный план выполнен по обмерам сторонней организации и может не учитывать все особенности помещения и иметь размеры, отличающиеся от реальных.
4) Перед началом строительных работ все размеры необходимо уточнить на месте.
5) Все выключатели, розетки, точечные светильники в санузле влагостойкие.
6) Все отверстия в санузле для электрики (розетки, выключатели) остаются на прежних местах.
7) Уточнить размеры профиля для светодиодной ленты для подсветки кухонной зоны.
8) Если уровень натяжного потолка будет ниже потолочных балок, то размещение потолочных светильников нужно изменить. Согласовать с дизайнером и заказчиками.
9) Все размеры указаны без учета отделочных материалов.
10) Согласовать с электриками размещение эл. щитка.

Условные обозначения:

- - - - светодиодная лента
- подвесной светильник в санузле - 2 шт
- встроенный потолочный светильник в санузле - 3 шт
- встроенный потолочный светильник в санузле в душевой- 1 шт
- встроенный потолочный светильник в прихожей - 3 шт
- встроенный настенный светильник в прихожей - 2 шт
- встроенный потолочный светильник в зоне спальни - 5 шт
- подвесной потолочный светильник у кровати в зоне спальни - 2 шт

Изм.	Кол.уч.	Лист	№Док.	Подп.	Дата	Room 381	Стадия	Лист	Листов
						План размещения светильников и их привязки к выключателям. М1:70			