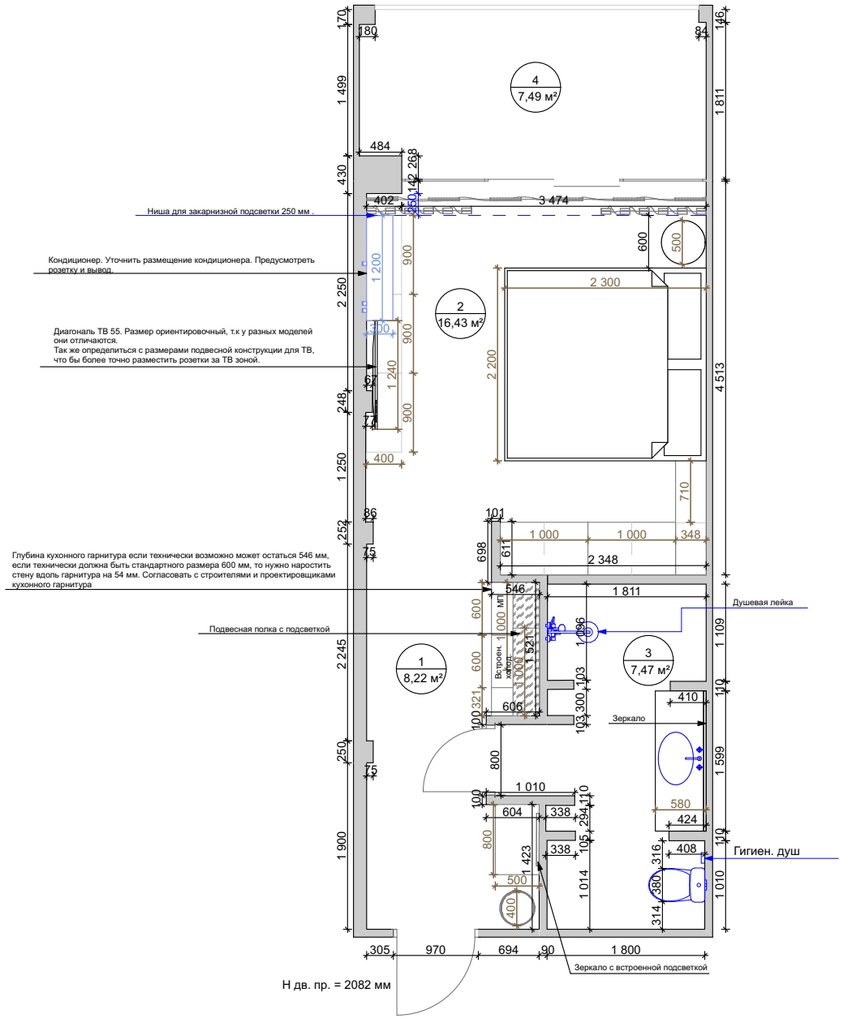
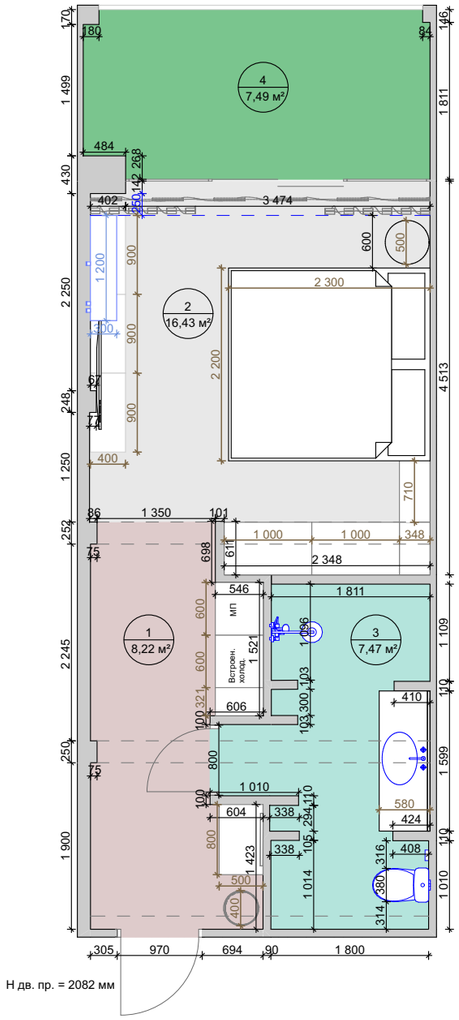



| № | Наименование | Площадь |
|---|---|---|
| 1 | Прихожая | 8,22 |
| 2 | Зона спальни | 16,43 |
| 3 | Санузел | 7,47 |
| 4 | Балкон | 7,49 |
| | | 39,61 м² |

Примечания:

Обязательно перепроверить размеры помещения, тк могут быть расхождения с обмерным планом!!!

1) Все размеры указаны без учета отделочных материалов.
2) Уточнить какой замок при входе в номер, и где размещать.
3)Обмерный план выполнен по обмерам сторонней организации и может не учитывать все особенности помещения и иметь размеры, отличающиеся от реальных.
4) Перед началом строительных работ все размеры необходимо уточнить на месте.
5) Утвердить открывание дверей.
6) Глубина кухонного гарнитура если технически возможно может остаться 546 мм, если технически должна быть стандартного размера 600 мм, то нужно наростить стену вдоль гарнитура на 54 мм. Согласовать с строителями и проектировщиками кухонного гарнитура.
7) Все уточнения, изменения по проекту согласовывать с заказчиком и дизайнером.

Условные обозначения:
- зона прихожей
- зона спальни
- санузел
- балкон

| Изм. | Кол.уч. | Лист | №Док. | Подп. | Дата | | | | |
|---|---|---|---|---|---|---|---|---|---|
| | | | | | | Room 381 | Стадия | Лист | Листов |
| | | | | | | План расстановки мебели. М1:70 | | | |