


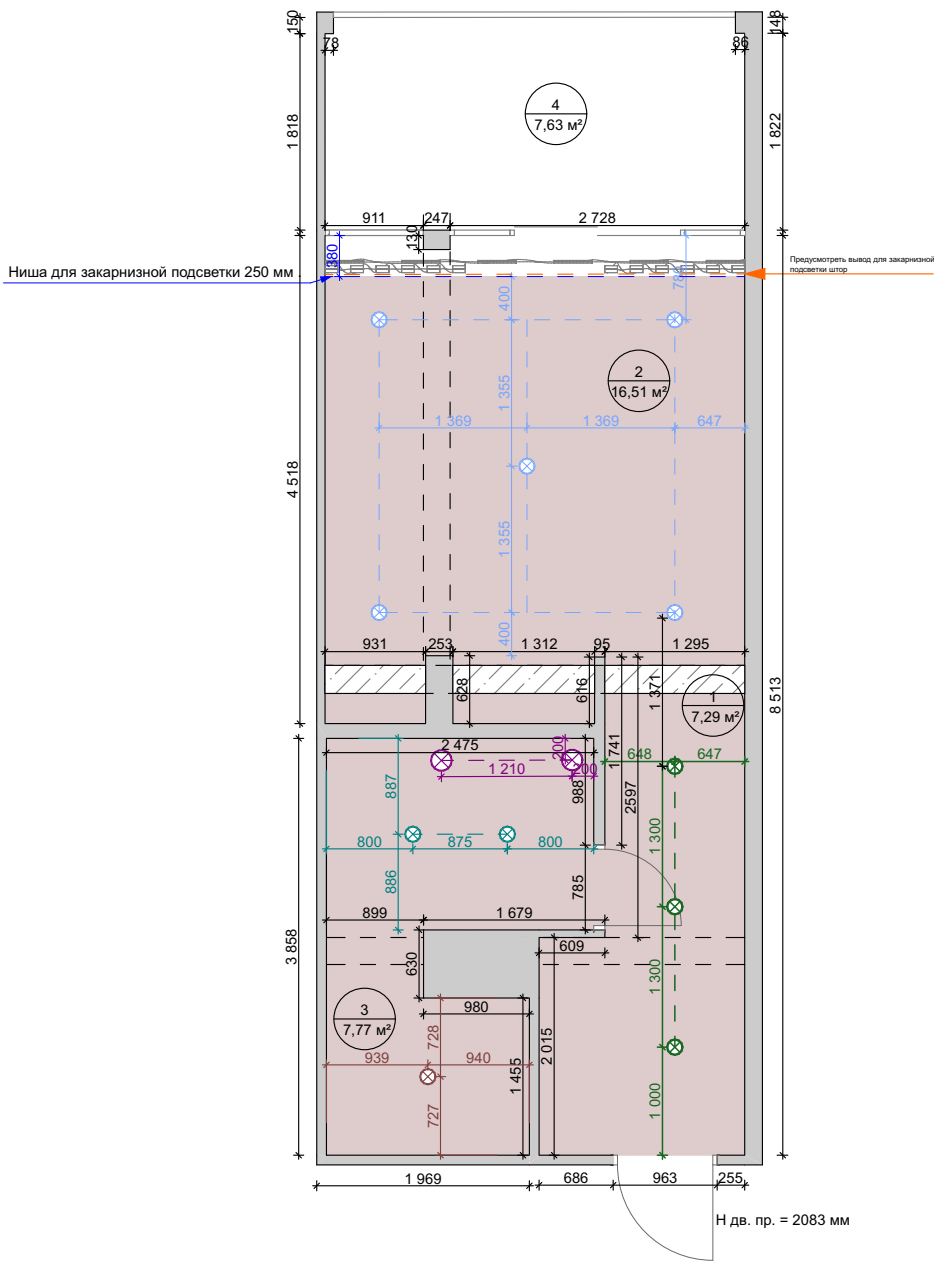

№	Наименование	Площадь
1	Прихожая	7,29
2	Зона спальни	16,51
3	Санузел	7,77
4	Балкон	7,63
		39,20 м²

Примечания:

- 1) Уточнить размещение кондиционеров, их управление (с пульта, или панель на стене).
- 2) Уточнить открывание дверей.
- 3) Обмерный план выполнен по обмерам сторонней организации и может не учитывать все особенности помещения и иметь размеры, отличающиеся от реальных.
- 4) Перед началом строительных работ все размеры необходимо уточнить на месте.
- 5) Все размеры указаны без учета отделочных материалов.

Условные обозначения:

- балка
- влагостойкий белый матовый натяжной потолок.
- светодиодная лента
- подвесной светильник в санузеле - 2 шт
- встроенный потолочный светильник в санузеле - 2 шт
- встроенный потолочный светильник в санузеле в душевой- 1 шт
- встроенный потолочный светильник в прихожей - 3 шт
- встроенный потолочный светильник в зоне гостиной - 5 шт

Изм.	Копуч.	Лист	№Док.	Подп.	Дата	Room 382	Стадия	Лист	Листов
						План потолка. M1:70			