


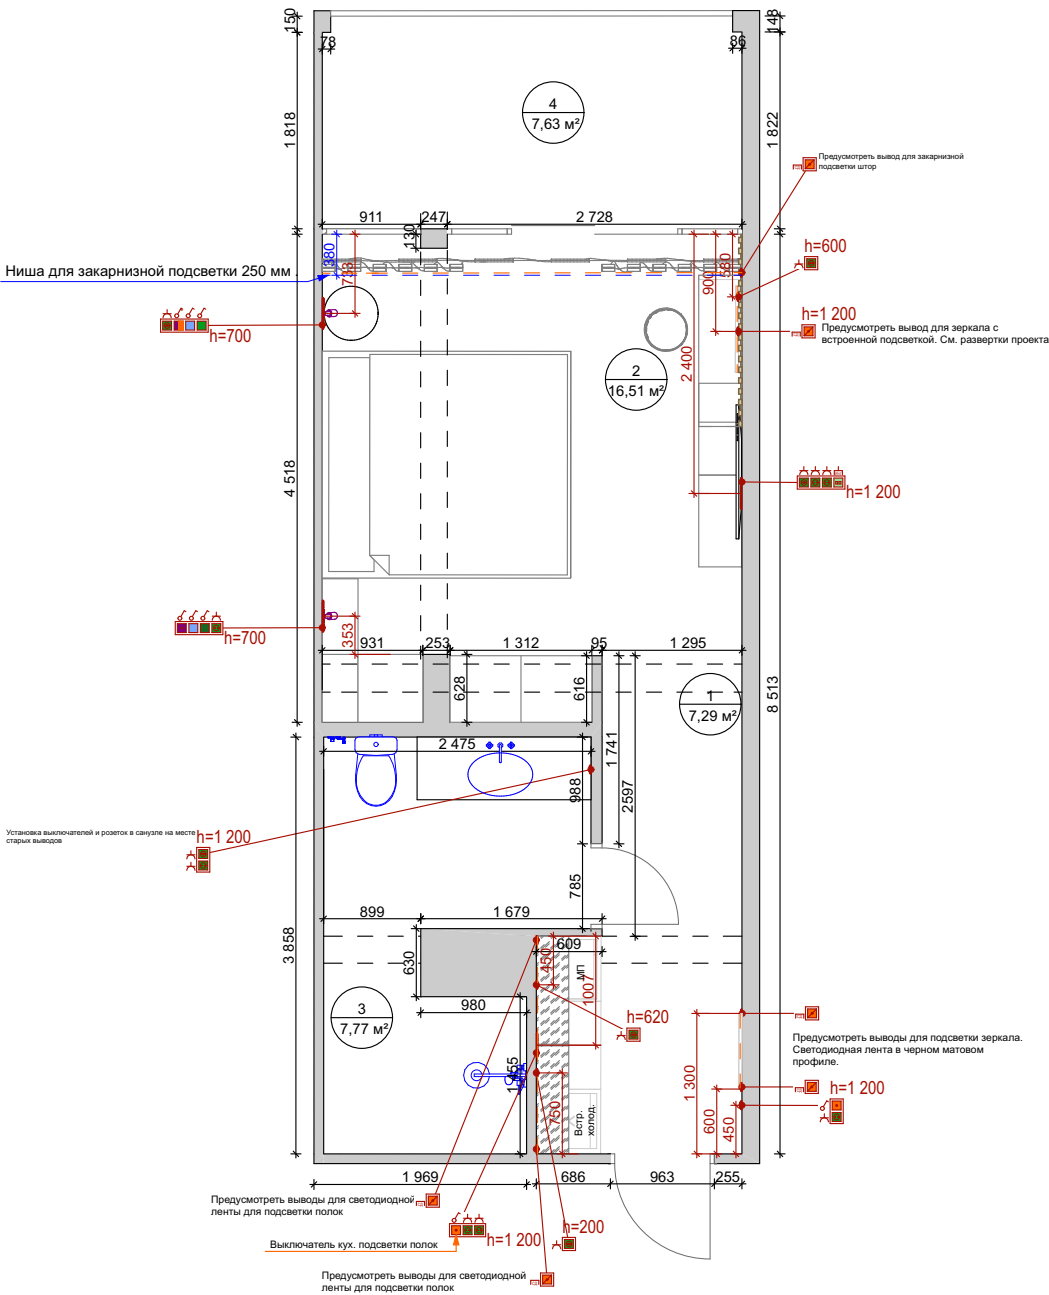

№	Наименование	Площадь
1	Прихожая	7,29
2	Зона спальни	16,51
3	Санузел	7,77
4	Балкон	7,63
		39,20 м²

Примечания:

Обязательно перепроверить размеры помещения, тк могут быть расхождения с обмерным планом!!!

- 1) Уточнить размещение кондиционеров, их управление (с пульта, или панель на стене).
- 2) Уточнить какой замок при входе в номер, и где размещать.
- 3) Обмерный план выполнен по обмерам сторонней организации и может не учитывать все особенности помещения и иметь размеры, отличающиеся от реальных.
- 4) Перед началом строительных работ все размеры необходимо уточнить на месте.
- 5) Все выключатели и розетки в санузле влагостойкие.
- 6) Все отверстия в санузле для электрики (розетки, выключатели) остаются на прежних местах.
- 7) Все размеры указаны без учета отделочных материалов.
- 8) Согласовать с электриками размещение эл.щитка.

Изм.	Копуч.	Лист	№Док.	Подп.	Дата				
						Room 382	Стадия	Лист	Листов
						План размещения розеток. М1:70			