
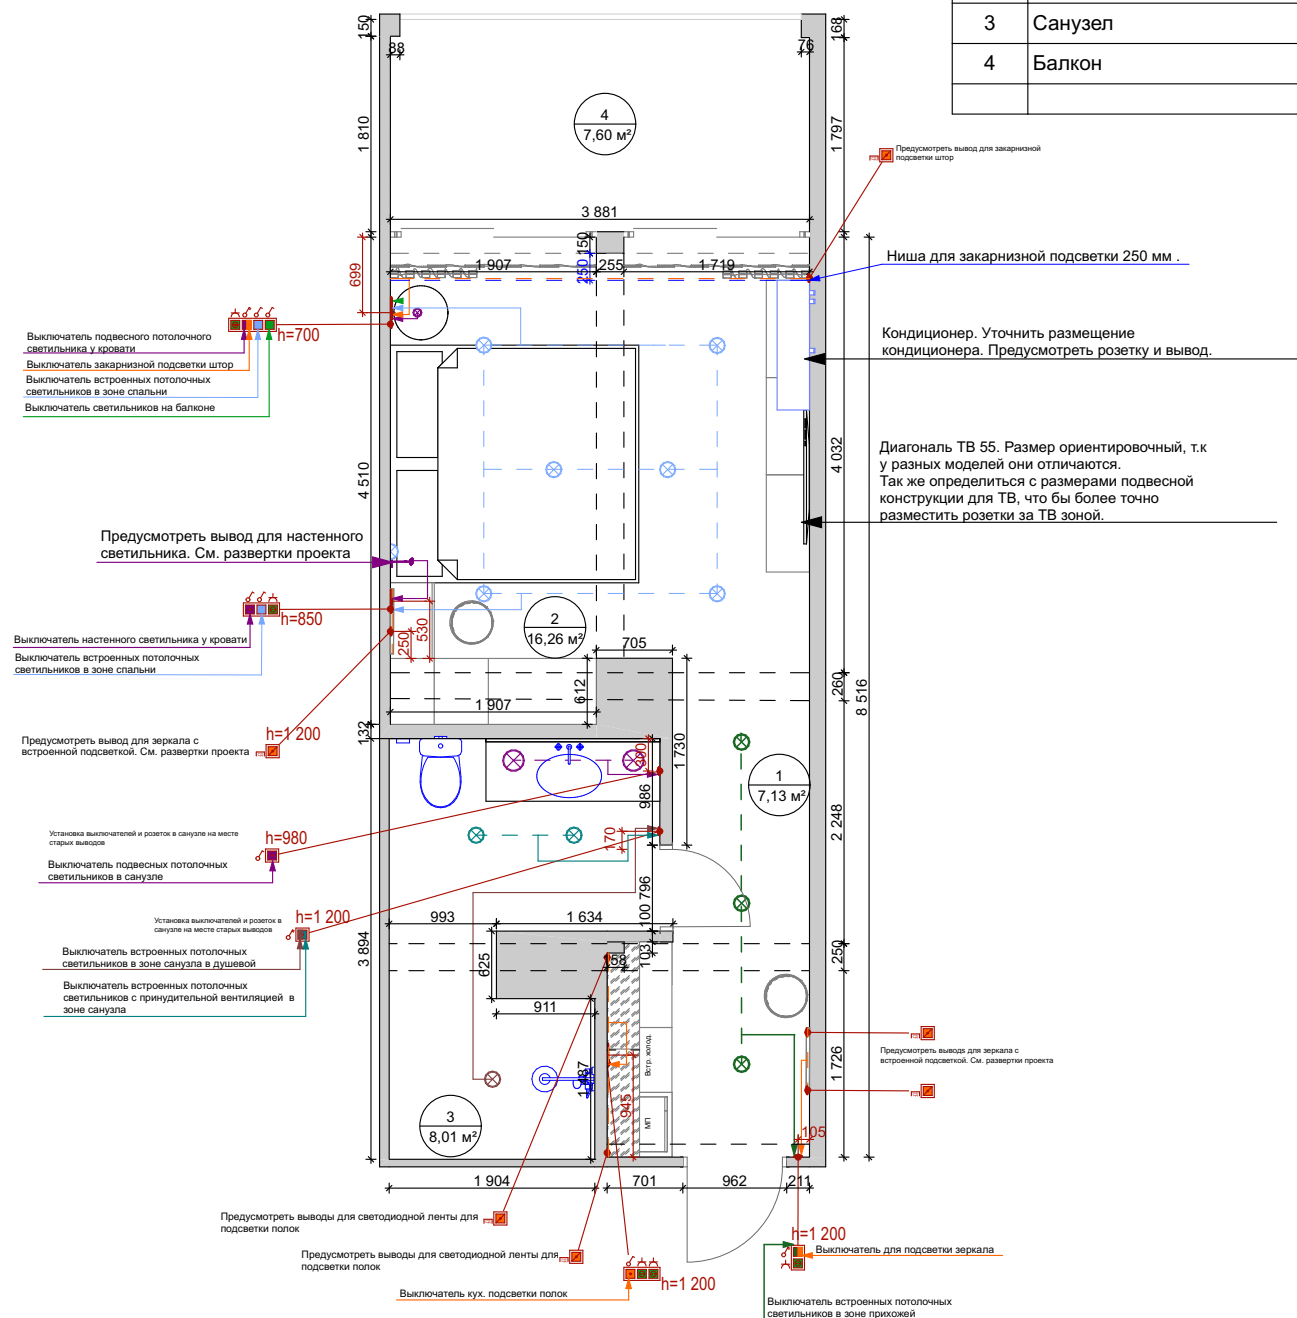


№	Наименование	Площадь
1	Прихожая	7,13
2	Зона спальни	16,26
3	Санузел	8,01
4	Балкон	7,60
		39,00 м²

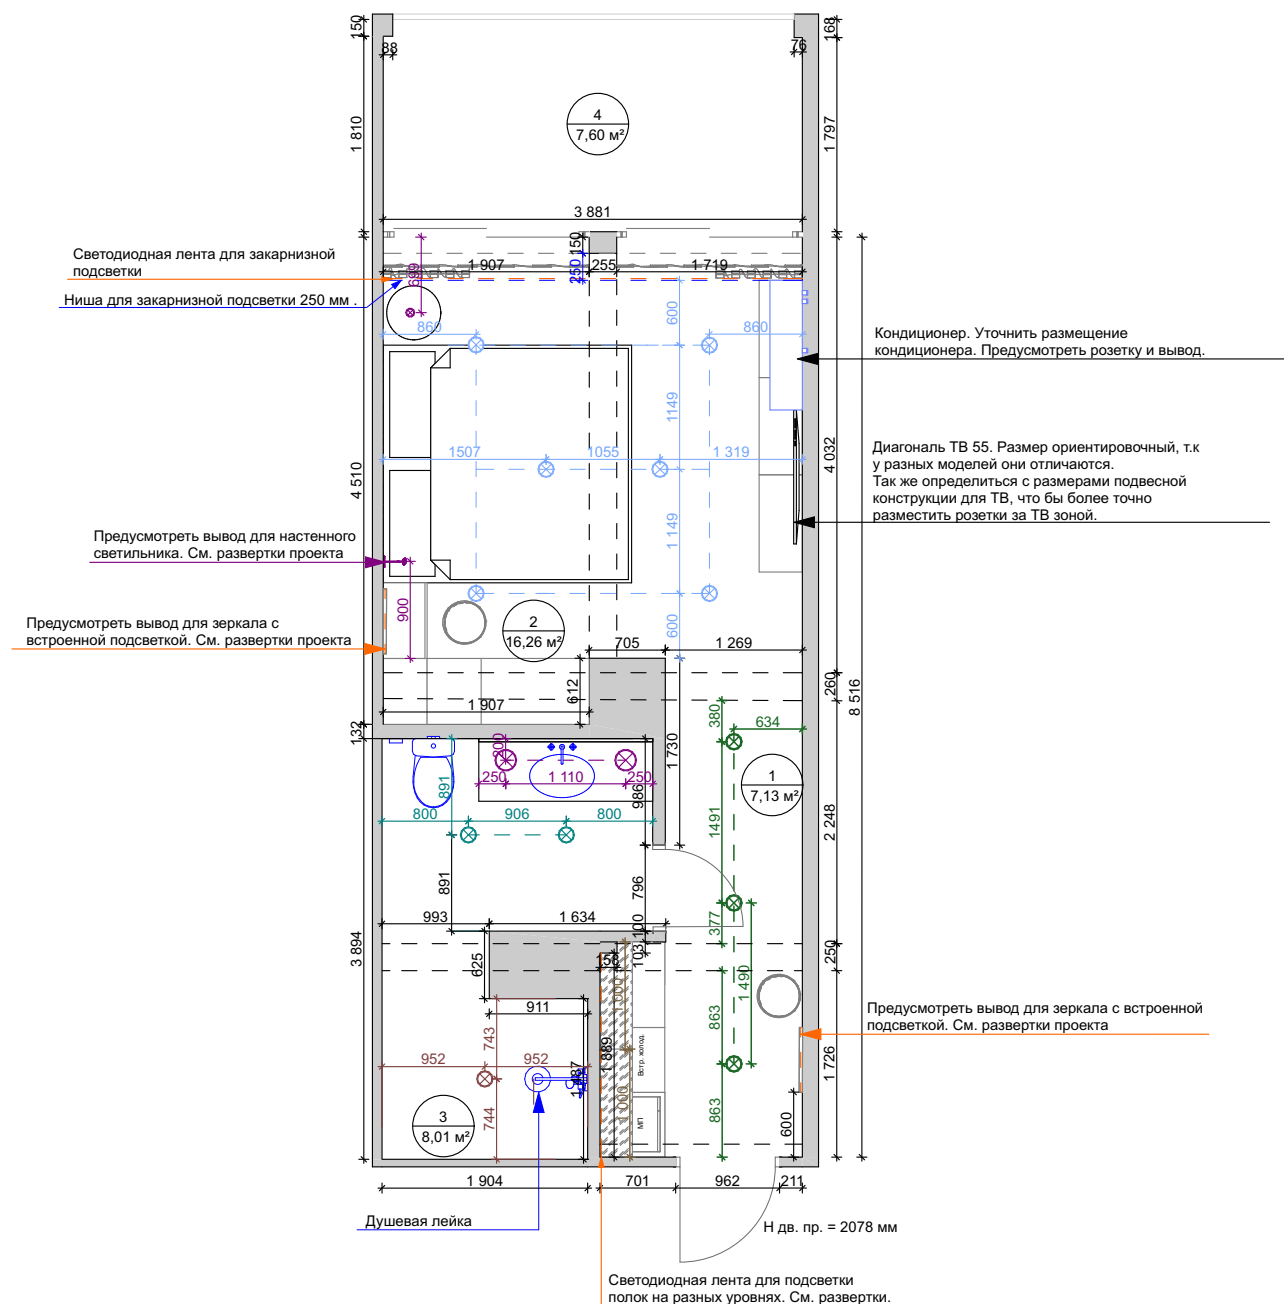

Примечания:

Обязательно перепроверить размеры помещения, тк могут быть расхождения с обмерным планом!!!

- 1) Уточнить размещение кондиционеров, их управление (с пульта, или панель на стене).
- 2) Уточнить какой замок при входе в номер, и где размещать.
- 3) Обмерный план выполнен по обмерам сторонней организации и может не учитывать все особенности помещения и иметь размеры, отличающиеся от реальных.
- 4) Перед началом строительных работ все размеры необходимо уточнить на месте.
- 5) Все выключатели, розетки, точечные светильники в санузле влагостойкие.
- 6) Все отверстия в санузле для электрики (розетки, выключатели) остаются на прежних местах.
- 7) Уточнить размеры профиля для светодиодной ленты для подсветки кухонной зоны.
- 8) Все размеры указаны без учета отделочных материалов.
- 9) Согласовать с электриками размещение эл. щитка.

Условные обозначения:

- - светодиодная лента
-  - подвесной светильник в санузле - 2 шт
-  - встроенный потолочный светильник в санузле - 2 шт
-  - встроенный потолочный светильник в санузле в душевой- 1 шт
-  - встроенный потолочный светильник в прихожей - 3 шт
-  - встроенный потолочный светильник в зоне спальни - 6 шт
-  - подвесной потолочный светильник у кровати - 1 шт
-  - настенный светильник - 1 шт

Изм.	Копуч.	Лист	№Док.	Подп.	Дата				
						Room 383	Стадия	Лист	Листов
						План размещения светильников и их привязки к выключателям. М1:70			