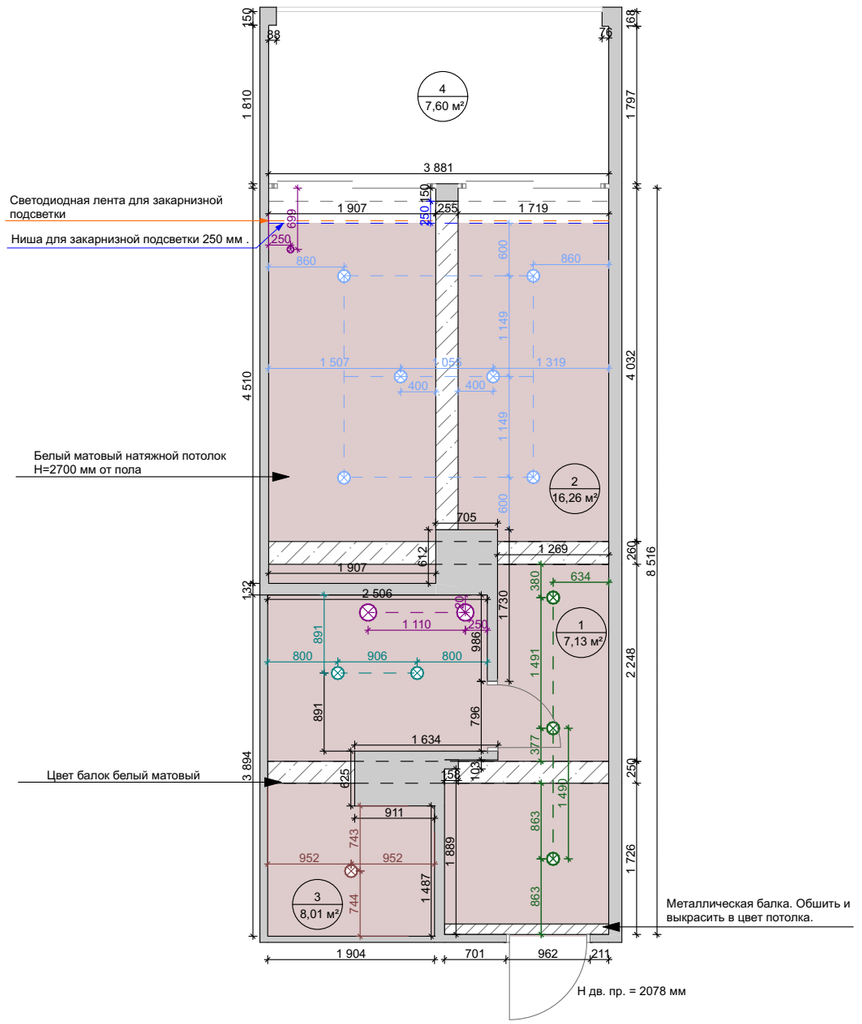

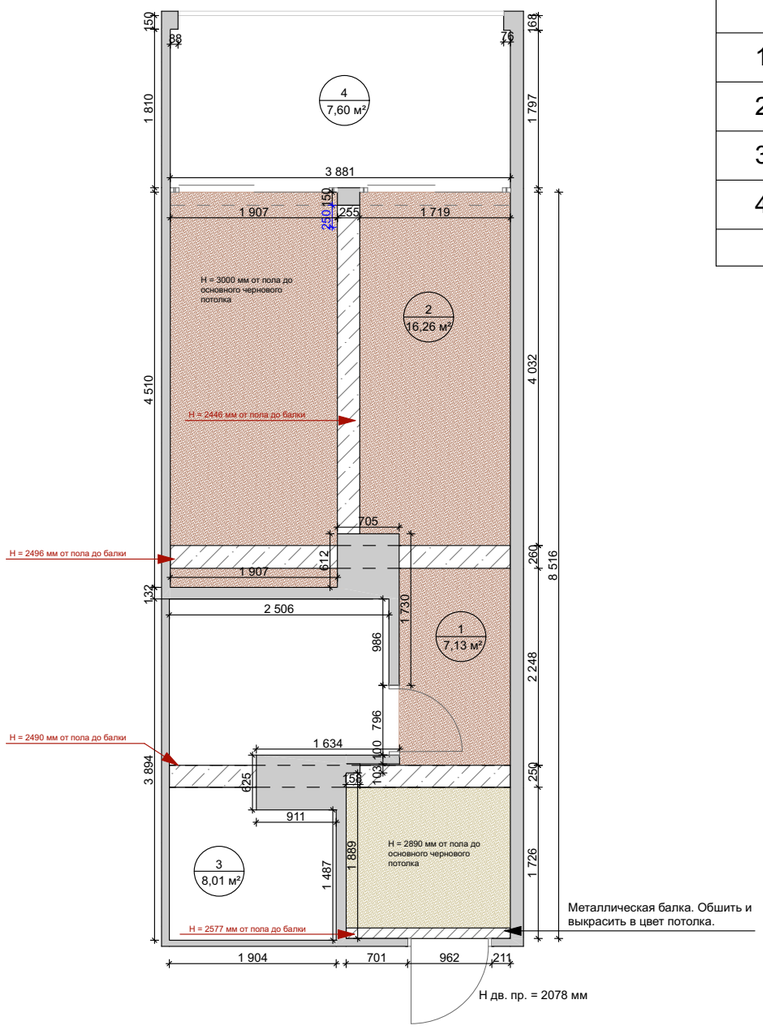

№	Наименование	Площадь
1	Прихожая	7,13
2	Зона спальни	16,26
3	Санузел	8,01
4	Балкон	7,60
		39,00 м²

Примечания:

1)Уточнить размещение кондиционеров, их управление (с пульта, или панель на стене).
2) Уточнить открывание дверей.
3)Обмерный план выполнен по обмерам сторонней организации и может не учитывать все особенности помещения и иметь размеры, отличающиеся от реальных.
4) Перед началом строительных работ все размеры необходимо уточнить на месте.
5) Все размеры указаны без учета отделочных материалов.

Условные обозначения:

- зона чернового потолка
- зона чернового потолка
- балка
- влагостойкий белый матовый натяжной потолок.
- светодиодная лента
- подвесной светильник в санузле - 2 шт
- встроенный потолочный светильник в санузле - 2 шт
- встроенный потолочный светильник в санузле в душевой- 1 шт
- встроенный потолочный светильник в прихожей - 3 шт
- встроенный потолочный светильник в зоне спальни - 6 шт
- подвесной потолочный светильник у кровати - 1 шт

Изм.	Кол.уч.	Лист	№Док.	Подп.	Дата				
						Room 383	Стадия	Лист	Листов
						План потолка. М1:70			