


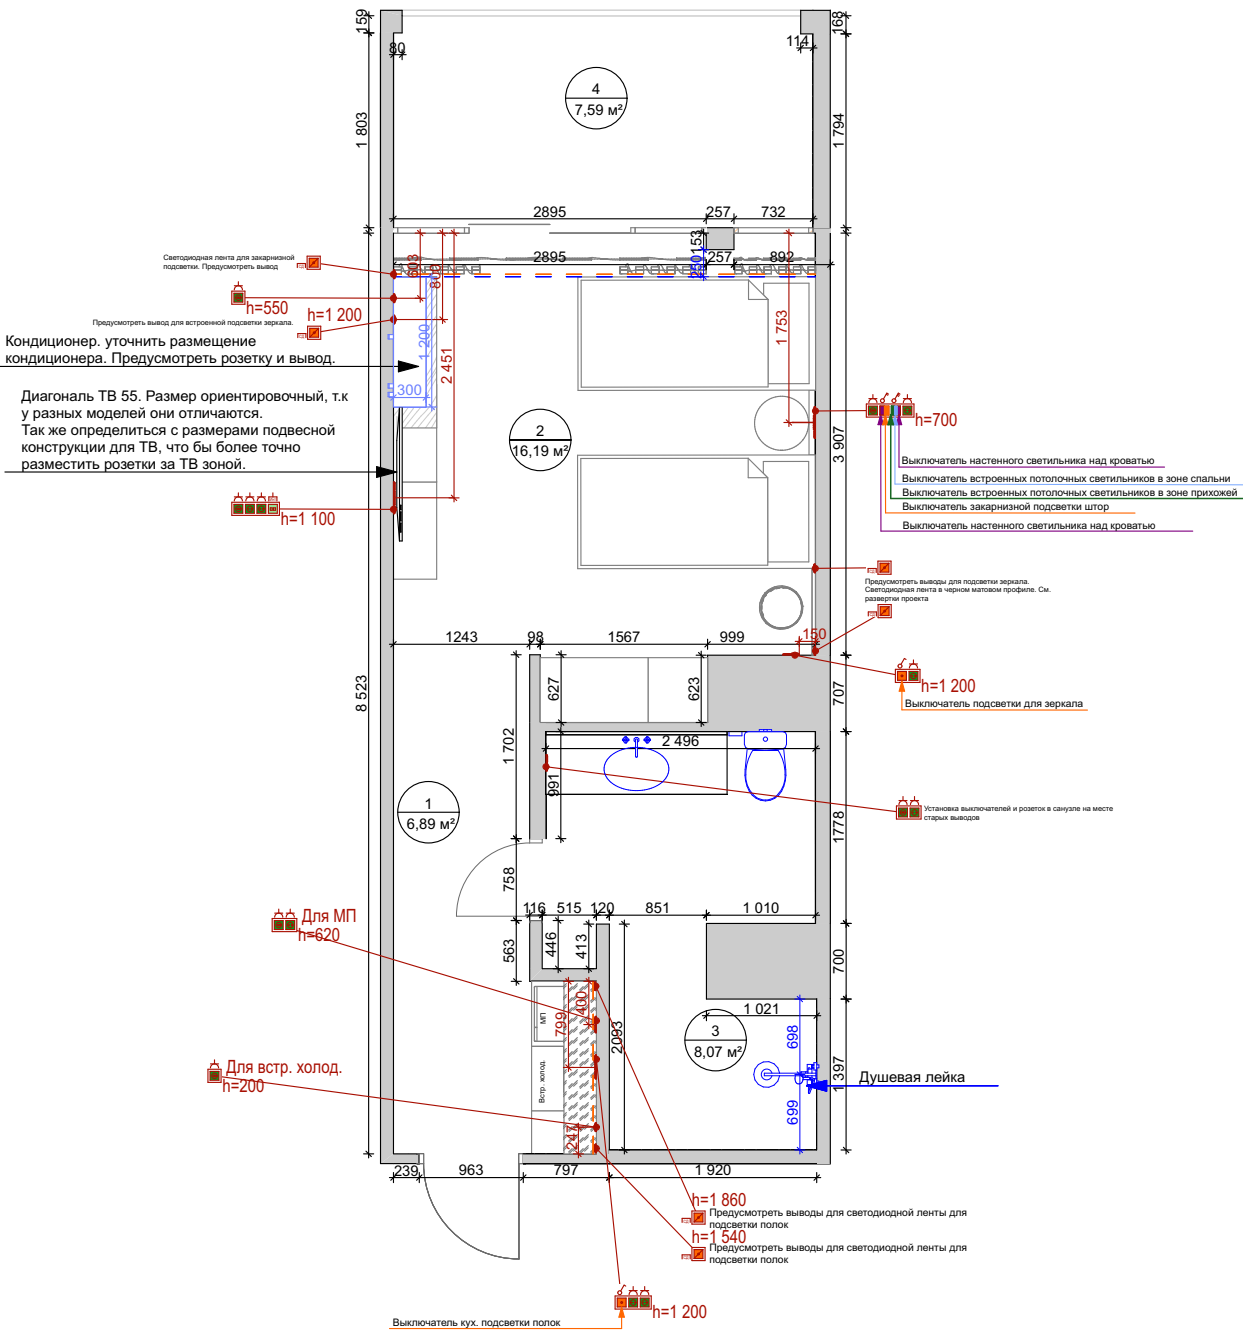

№	Наименование	Площадь
1	Прихожая	6,89
2	Зона спальни	16,19
3	Санузел	8,07
4	Балкон	7,59
		38,74 м²

- Примечания:
- Обязательно перепроверить размеры помещения, тк могут быть расхождения с обмерным планом!!!
- 1) Уточнить размещение кондиционеров, их управление (с пульта, или панель на стене).
 - 2) Уточнить какой замок при входе в номер, и где размещать.
 - 3) Обмерный план выполнен по обмерам сторонней организации и может не учитывать все особенности помещения и иметь размеры, отличающиеся от реальных.
 - 4) Перед началом строительных работ все размеры необходимо уточнить на месте.
 - 5) Все выключатели и розетки в санузле влагостойкие.
 - 6) Все отверстия в санузле для электрики (розетки, выключатели) остаются на прежних местах.
 - 7) Уточнить размеры профиля для светодиодной ленты для подсветки кухонной зоны.
 - 8) Уточнить размеры настенных декоративных реек.
 - 9) Все размеры указаны без учета отделочных материалов.
 - 10) Согласовать с электриками размещение эл.щитка.

Изм.	Копуч.	Лист	№Док.	Подп.	Дата	Room 384	Стадия	Лист
								Листов
						План размещения розеток. М1:70		