


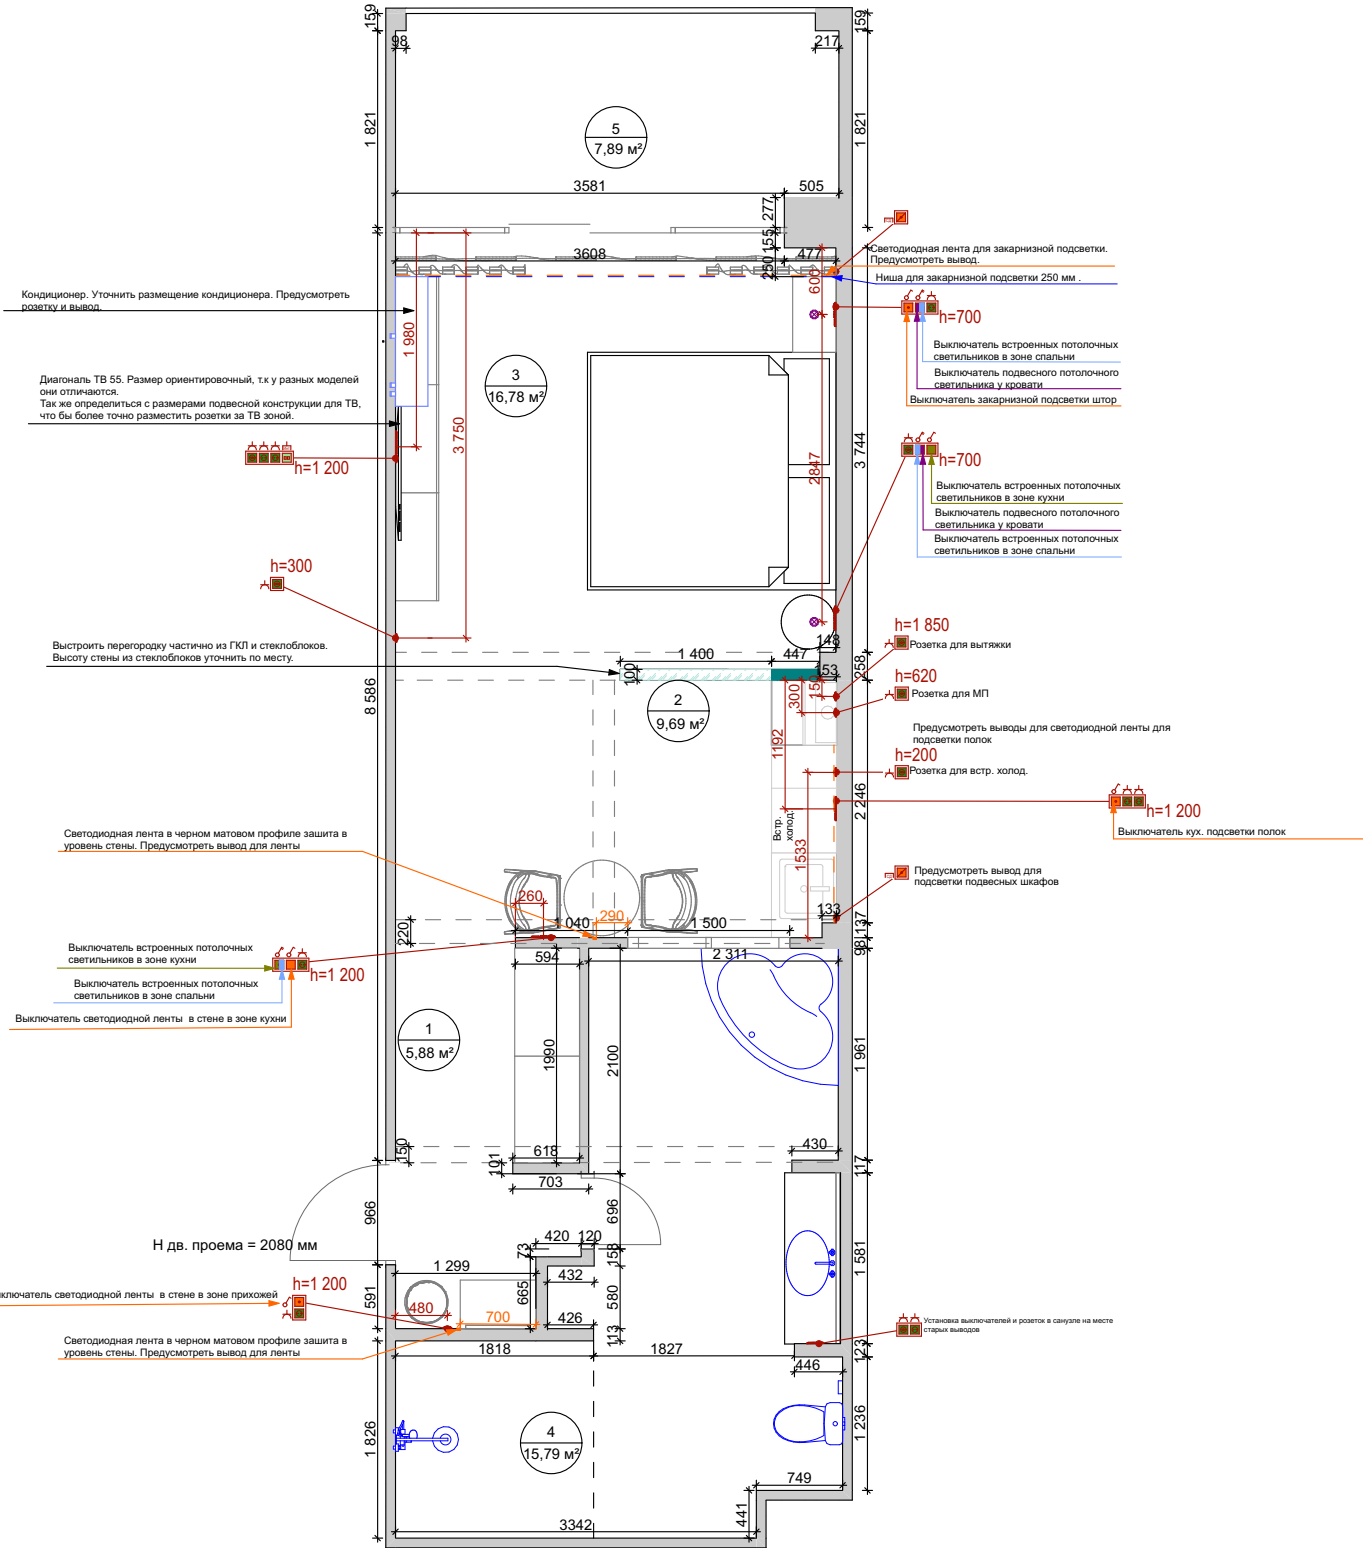

| № | Наименование | Площадь  |
|---|--------------|----------|
| 1 | Прихожая     | 5,88     |
| 2 | Зона кухни   | 9,69     |
| 3 | Зона спальни | 16,78    |
| 4 | Санузел      | 15,79    |
| 5 | Балкон       | 7,89     |
|   |              | 56,03 м² |

Примечания:

Обязательно перепроверить размеры помещения, тк могут быть расхождения с обмерным планом!!!

- 1) Уточнить размещение кондиционеров, их управление ( с пульта, или панель на стене).
- 2) Уточнить какой замок при входе в номер, и где размещать.
- 3) Обмерный план выполнен по обмерам сторонней организации и может не учитывать все особенности помещения и иметь размеры, отличающиеся от реальных.
- 4) Перед началом строительных работ все размеры необходимо уточнить на месте.
- 5) Все выключатели и розетки в санузле влагостойкие.
- 6) Все отверстия в санузле для электрики ( розетки, выключатели) остаются на прежних местах.
- 7) Уточнить размеры профиля для светодиодной ленты.
- 8) Все размеры указаны без учета отделочных материалов.
- 9) Согласовать с электриками размещение эл.щитка.

|      |        |      |       |       |      |                                |        |      |        |
|------|--------|------|-------|-------|------|--------------------------------|--------|------|--------|
|      |        |      |       |       |      |                                |        |      |        |
|      |        |      |       |       |      |                                |        |      |        |
|      |        |      |       |       |      |                                |        |      |        |
| Изм. | Копуч. | Лист | №Док. | Подп. | Дата | Room 385                       | Стадия | Лист | Листов |
|      |        |      |       |       |      |                                |        |      |        |
|      |        |      |       |       |      |                                |        |      |        |
|      |        |      |       |       |      |                                |        |      |        |
|      |        |      |       |       |      | План размещения розеток. М1:70 |        |      |        |
|      |        |      |       |       |      |                                |        |      |        |
|      |        |      |       |       |      |                                |        |      |        |