


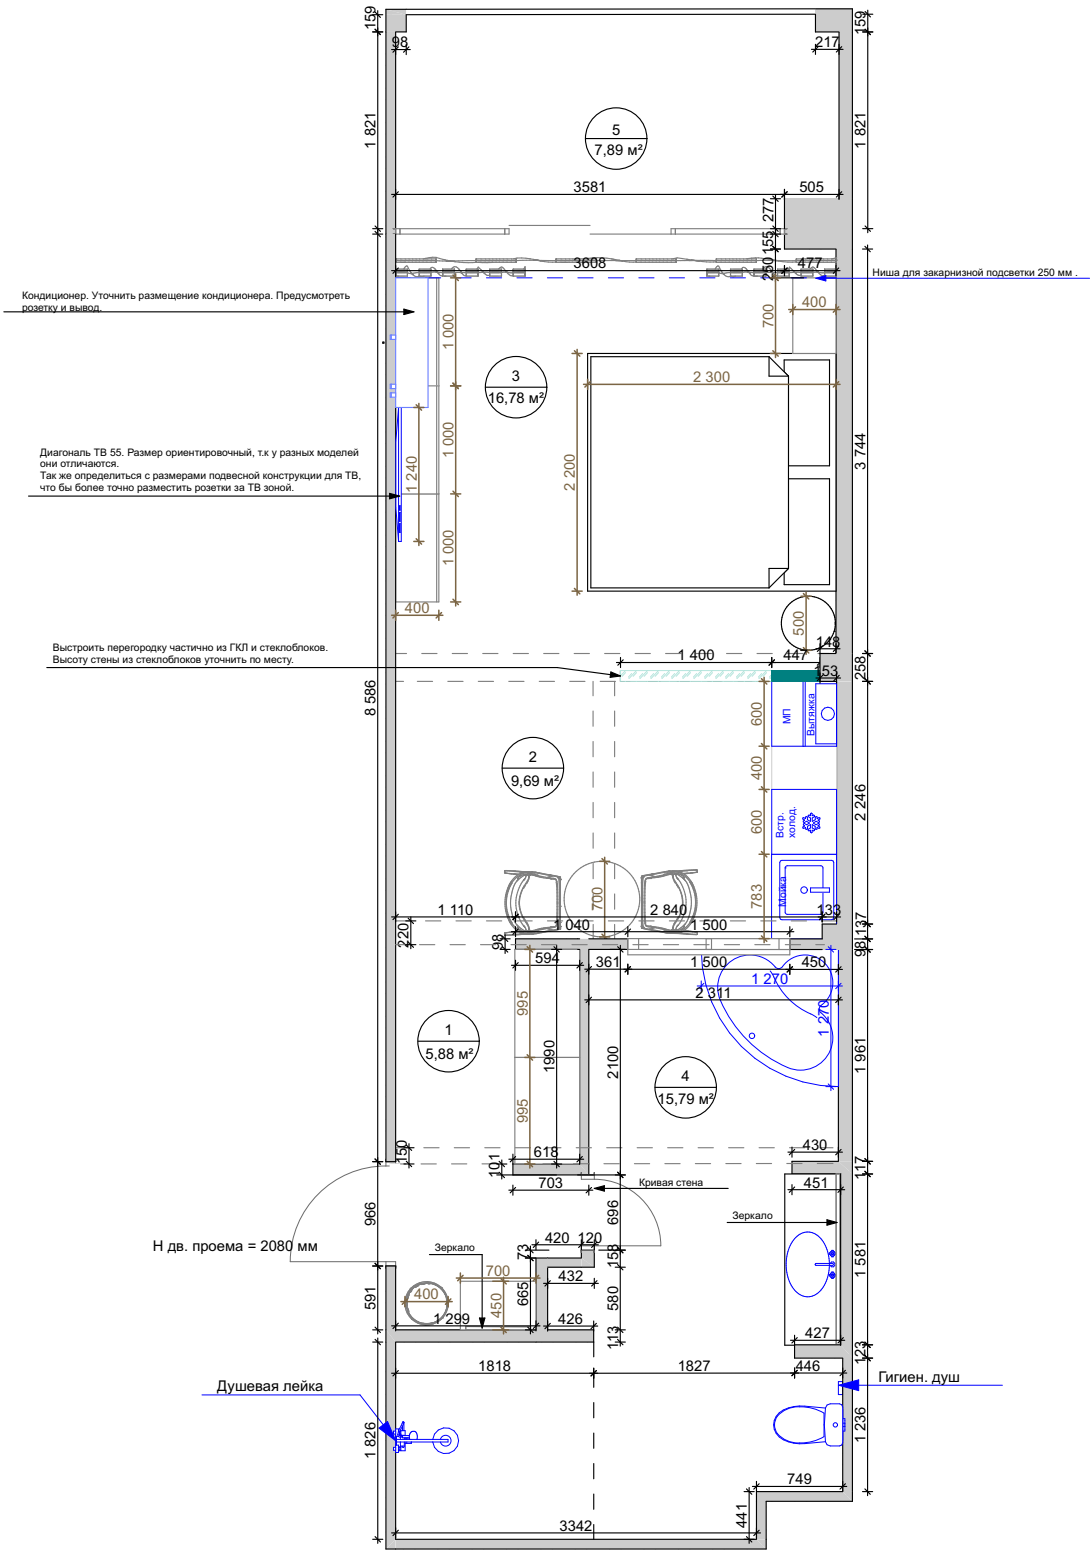

№	Наименование	Площадь
1	Прихожая	5,88
2	Зона кухни	9,69
3	Зона спальни	16,78
4	Санузел	15,79
5	Балкон	7,89
		56,03 м²

- Примечания:
- Обязательно перепроверить размеры помещения, тк могут быть расхождения с обмерным планом!!!
- 1)Уточнить размещение кондиционеров, их управление (с пульта, или панель на стене).
 - 2) Уточнить какой замок при входе в номер, и где размещать.
 - 3)Обмерный план выполнен по обмерам сторонней организации и может не учитывать все особенности помещения и иметь размеры, отличающиеся от реальных.
 - 4) Перед началом строительных работ все размеры необходимо уточнить на месте.
 - 5) Все размеры указаны без учета отделочных материалов.
 - 6) Сантехническое оборудование в санузле находится на прежних местах.

Изм.	Копуч.	Лист	№Док.	Подп.	Дата	Room 385	Стадия	Лист	Листов
						План размещения сантехнического и электрооборудования. М1:70			