
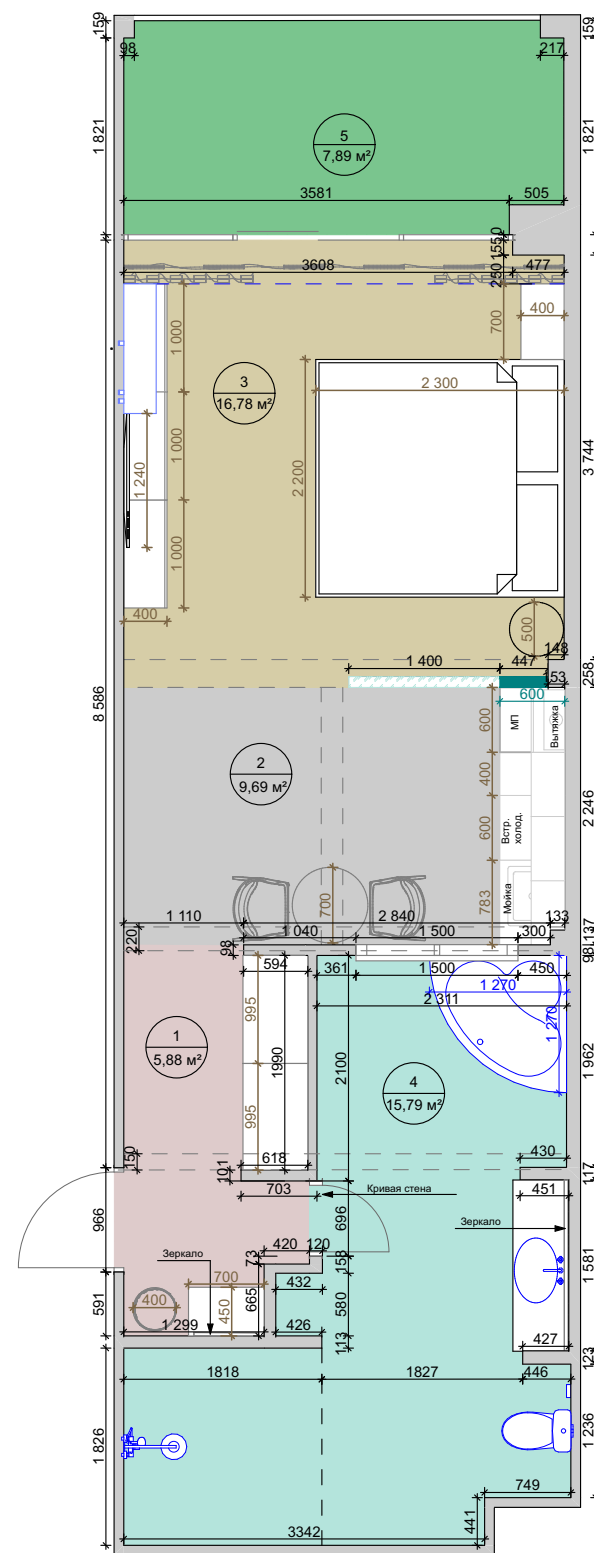


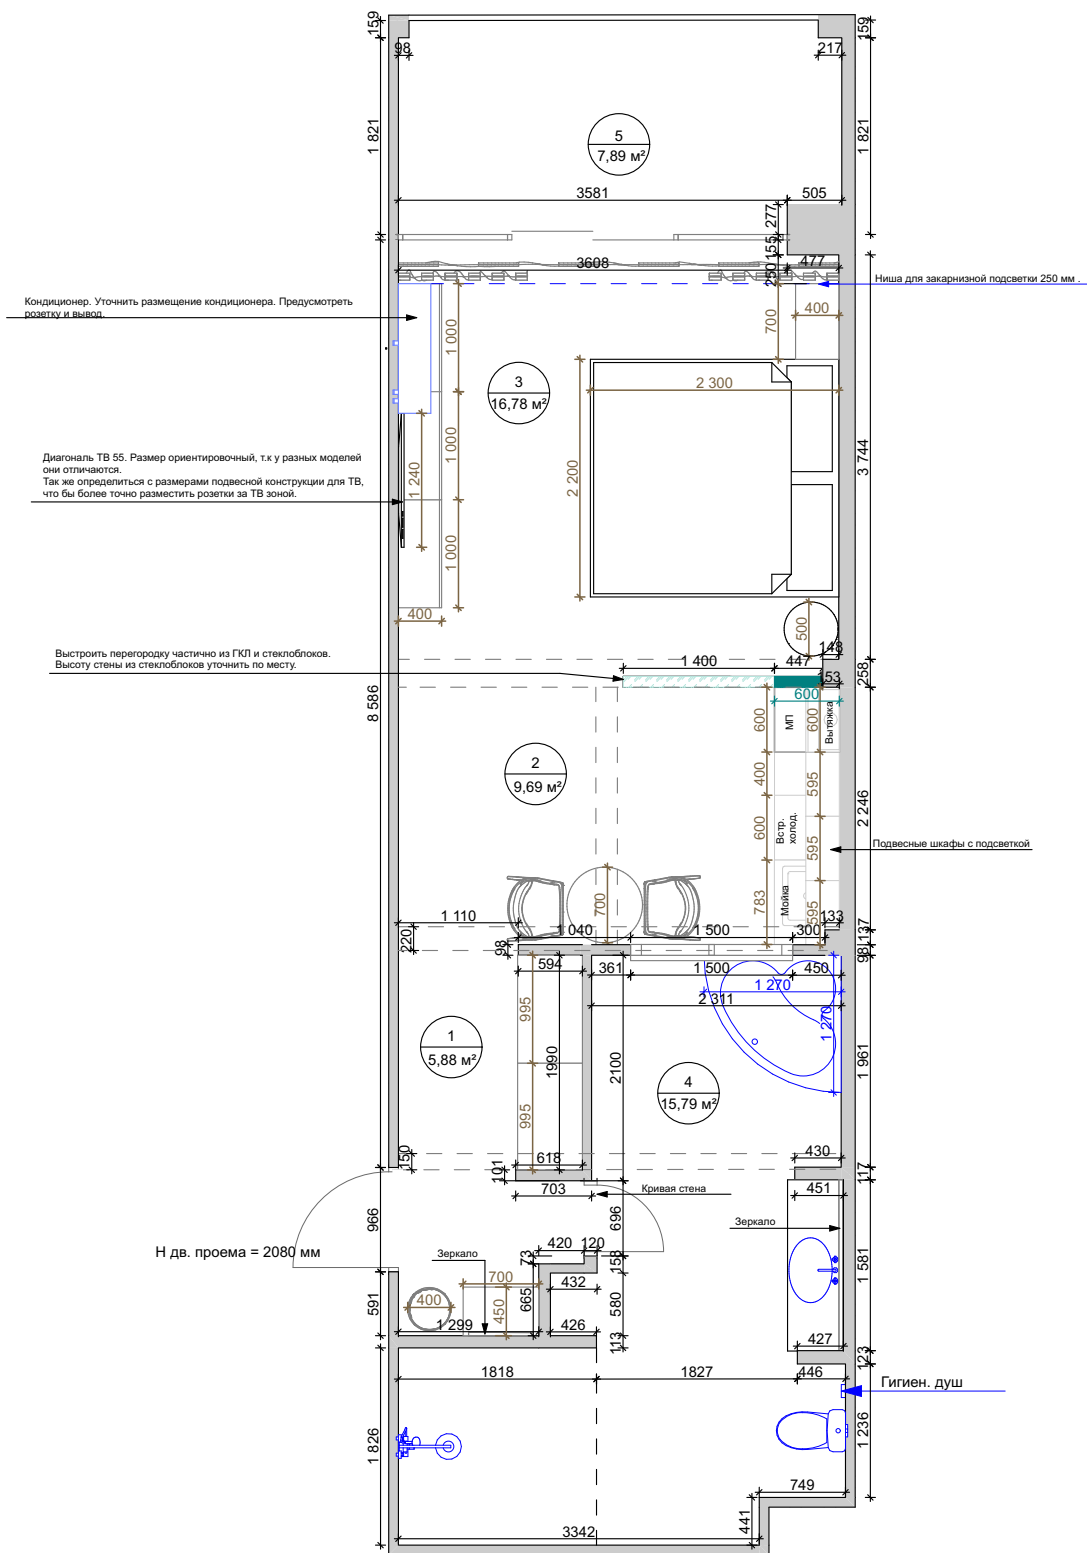

№	Наименование	Площадь
1	Прихожая	5,88
2	Зона кухни	9,69
3	Зона спальни	16,78
4	Санузел	15,79
5	Балкон	7,89
		56,03 м²

Примечания:

Обязательно перепроверить размеры помещения, тк могут быть расхождения с обмерным планом!!!

- 1) Все размеры указаны без учета отделочных материалов.
- 2) Уточнить какой замок при входе в номер, и где размещать.
- 3) Обмерный план выполнен по обмерам сторонней организации и может не учитывать все особенности помещения и иметь размеры, отличающиеся от реальных.
- 4) Перед началом строительных работ все размеры необходимо уточнить на месте.
- 5) Утвердить открывание дверей.
- 6) Перегородку частично выстроить из ГКЛ и стеклоблоков. Высоту стены из стеклоблоков уточнить по месту.
- 6) Все уточнения, изменения по проекту согласовывать с заказчиком и дизайнером.

Изм.	Копуч.	Лист	№Док.	Подп.	Дата				
						Room 385	Стадия	Лист	Листов
						План расстановки мебели. М1:70			