



№	Наименование	Площадь
1	Зона прихожей	8,05
2	Зона гостиной	16,87
3	Санузел	6,29
4	Балкон	7,44
		38,65 м²

Примечания:

- 1) Уточнить размещение кондиционеров, их управление (с пульта, или панель на стене).
2) Уточнить открывание дверей.
3) Обмерный план выполнен по обмерам сторонней организации и может не учитывать все особенности помещения и иметь размеры, отличающиеся от реальных.
4) Перед началом строительных работ все размеры необходимо уточнить на месте.
5) Все размеры указаны без учета отделочных материалов.

Условные обозначения:

-  - балка
-  - влагостойкий белый матовый натяжной потолок.
-  - светодиодная лента
-  - подвесной светильник в санузле - 2 шт
-  - встроенный потолочный светильник в санузле - 3 шт
-  - встроенный потолочный светильник в санузле в душевой- 1 шт
-  - встроенный потолочный светильник в прихожей - 3 шт
-  - встроенный потолочный светильник в зоне гостиной - 5 шт
-  - подвесной потолочный светильник над барным столом в зоне гостиной - 2 шт

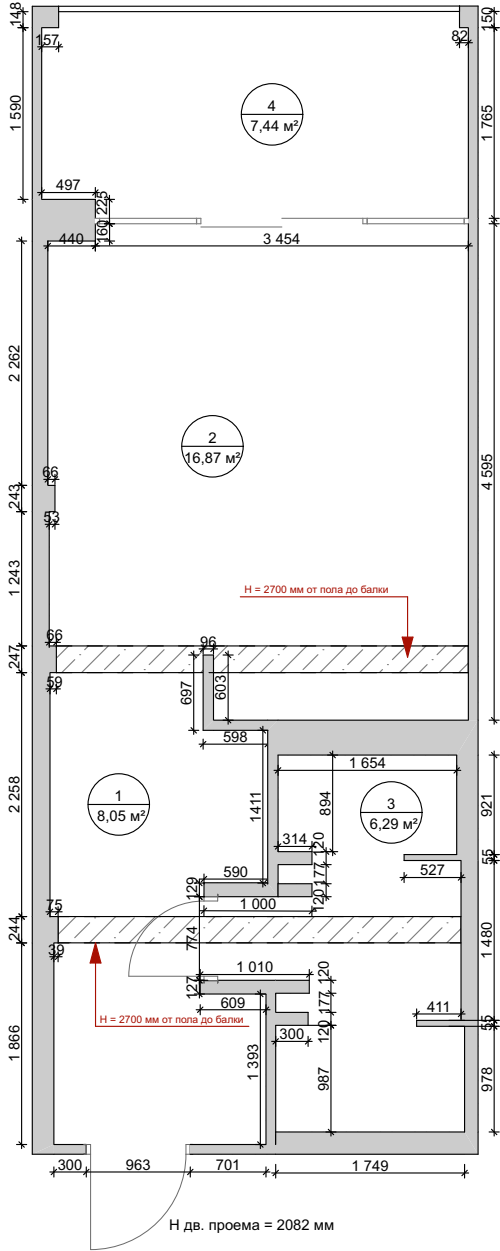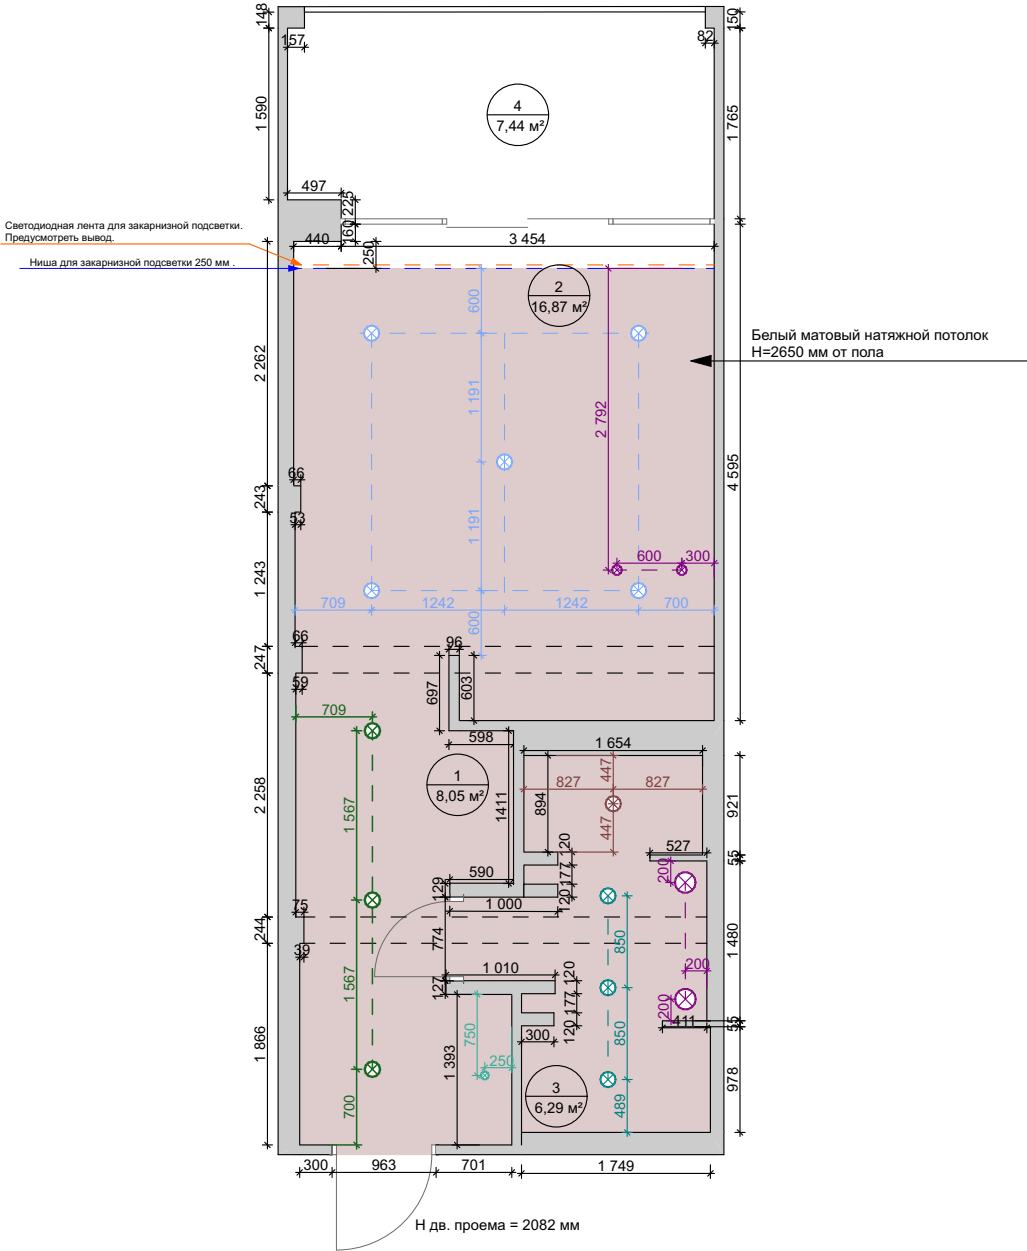

Изм.	Копуч.	Лист	№Док.	Подп.	Дата				
						Room 481	Стадия	Лист	Листов
						План потолка. M1:70			