


Диагональ ТВ 55. Размер ориентировочный, т.к у разных моделей они отличаются.
Так же определиться с размерами подвесной конструкции для ТВ, что бы более точно разместить розетки за ТВ зоной.

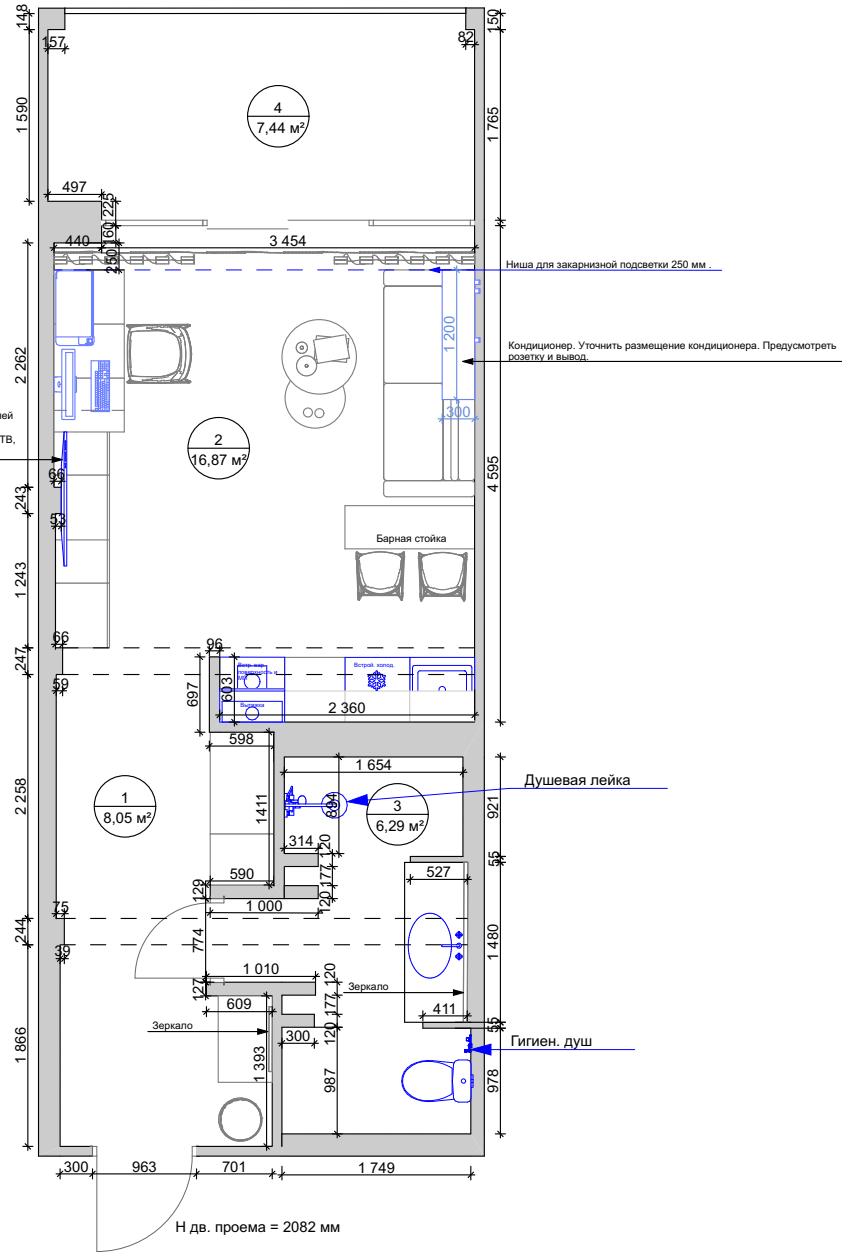

№	Наименование	Площадь
1	Зона прихожей	8,05
2	Зона гостиной	16,87
3	Санузел	6,29
4	Балкон	7,44
		38,65 м²

Изм.	Копуч.	Лист	№Док.	Подп.	Дата	Room 481	Стадия	Лист	Листов
						План размещения сантехнического и электрооборудования. М1:70			