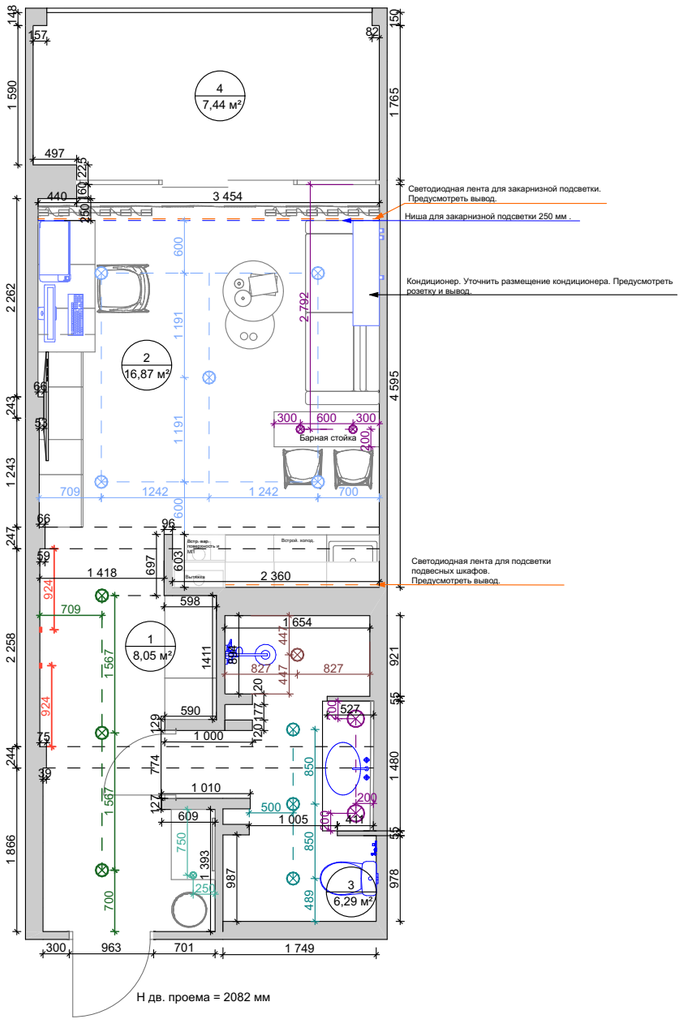

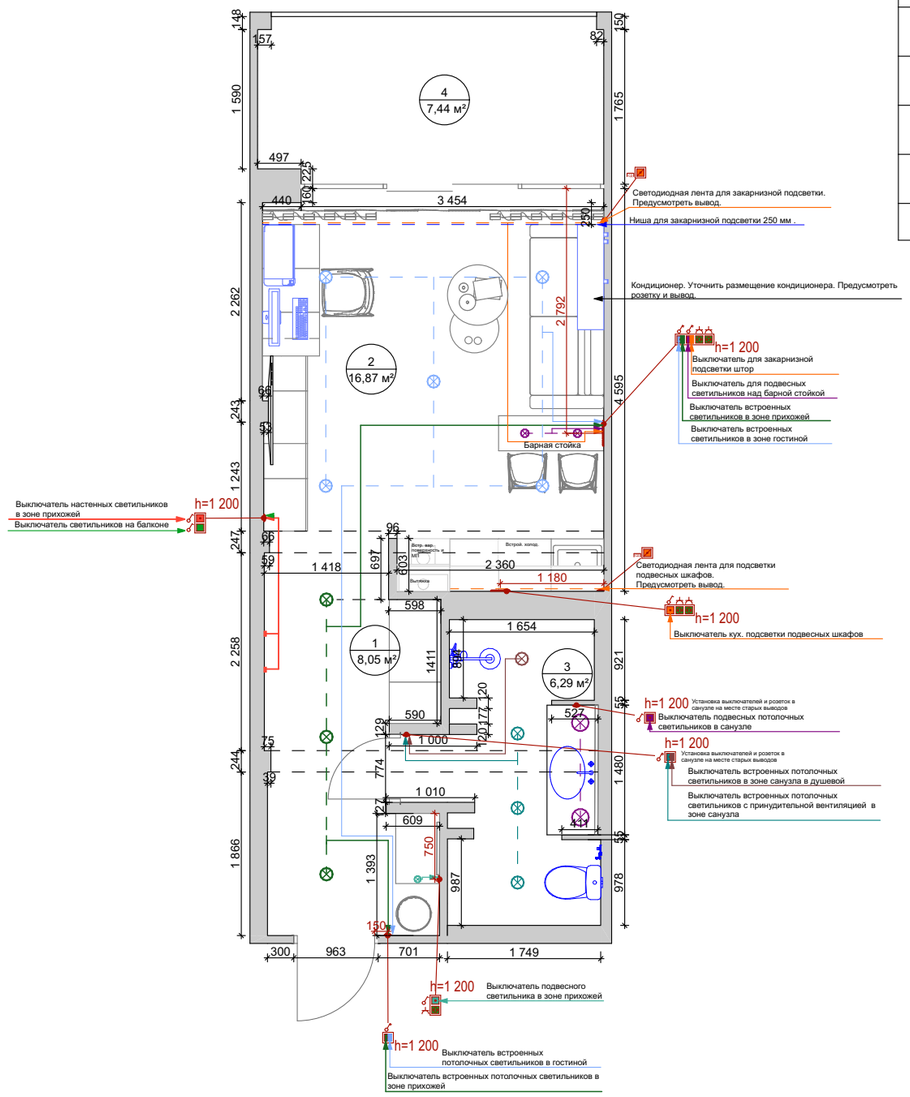

№	Наименование	Площадь
1	Зона прихожей	8,05
2	Зона гостиной	16,87
3	Санузел	6,29
4	Балкон	7,44
		38,65 м²

Примечания:

Обязательно перепроверить размеры помещения, тк могут быть расхождения с обмерным планом!!!

1)Уточнить размещение кондиционеров, их управление (с пульта, или панель на стене).
2) Уточнить какой замок при входе в номер, и где размещать.
3)Обмерный план выполнен по обмерам сторонней организации и может не учитывать все особенности помещения и иметь размеры, отличающиеся от реальных.
4) Перед началом строительных работ все размеры необходимо уточнить на месте.
5) Все выключатели, розетки, точечные светильники в санузле влагостойкие.
6) Все отверстия в санузле для электрики (розетки, выключатели) остаются на прежних местах.
7) Все размеры указаны без учета отделочных материалов.
8) Согласовать с электриками размещение эл. щитка.

Условные обозначения:

- светодиодная лента
- подвесной светильник в санузле - 2 шт
- встроенный потолочный светильник в санузле - 3 шт
- встроенный потолочный светильник в санузле в душевой- 1 шт
- встроенный потолочный светильник в прихожей - 3 шт
- встроенный настенный светильник в прихожей - 2 шт
- встроенный потолочный светильник в зоне гостиной - 5 шт
- подвесной потолочный светильник над барным столом в зоне гостиной - 2 шт

Изм.	Кол.уч.	Лист	№Док.	Подп.	Дата				
						Room 481	Стадия	Лист	Листов
						План размещения светильников и их привязки к выключателям. М1:70			