
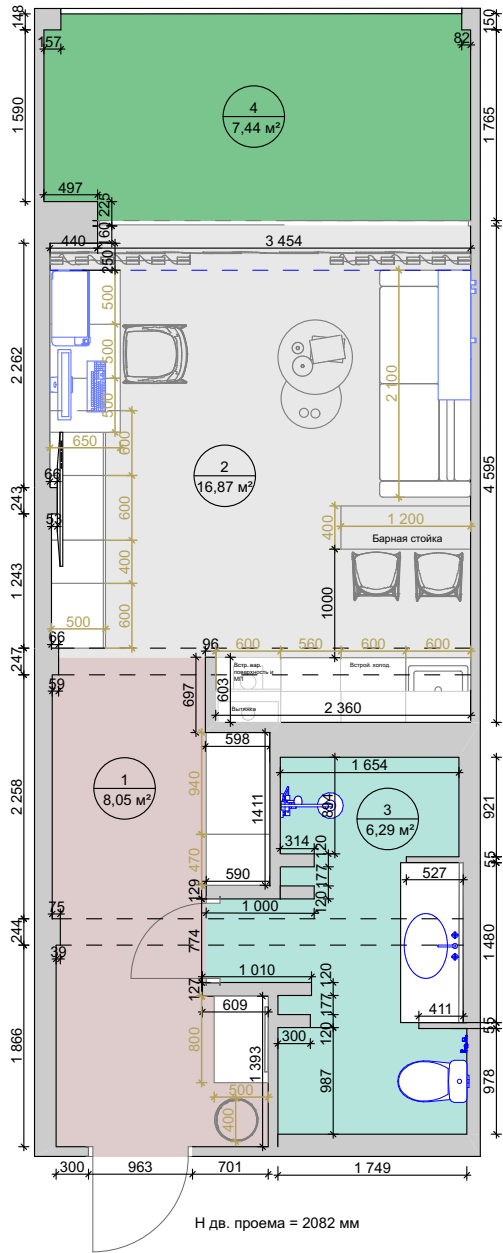


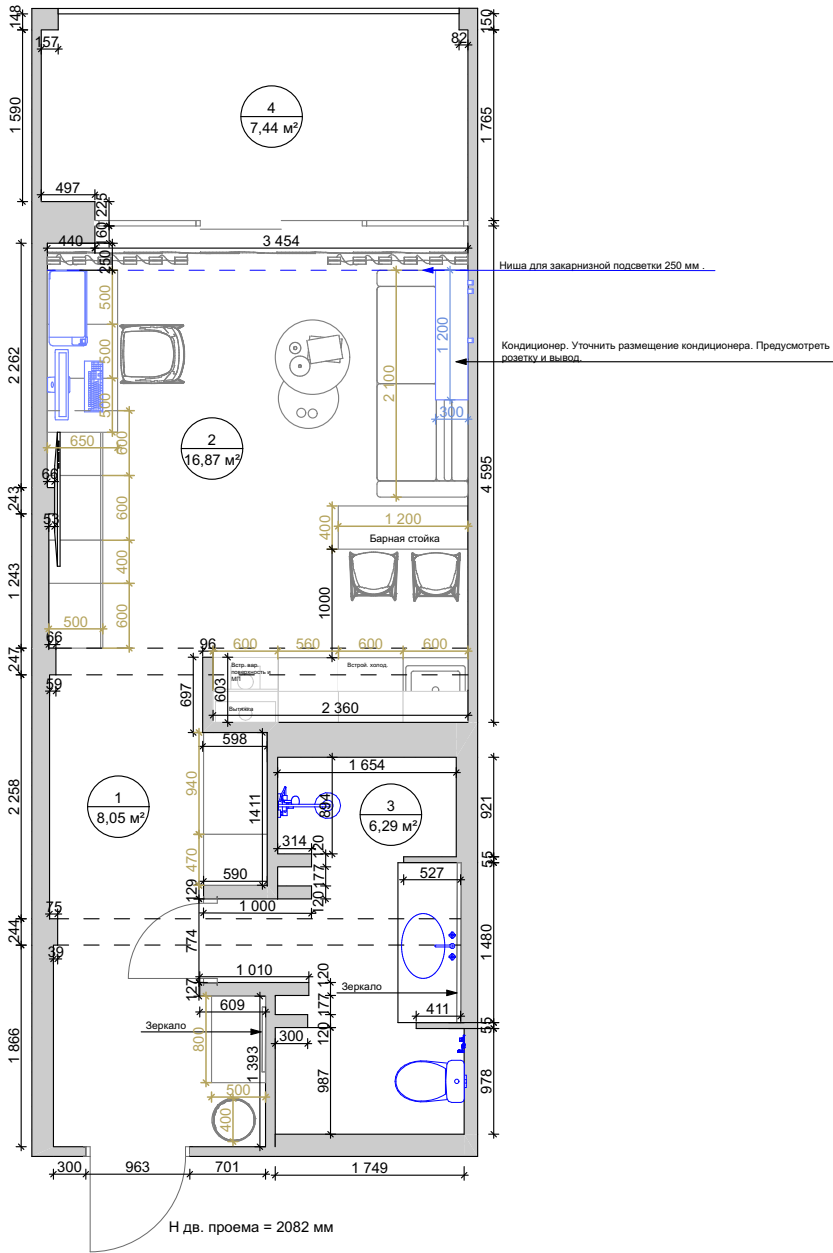

№	Наименование	Площадь
1	Зона прихожей	8,05
2	Зона гостиной	16,87
3	Санузел	6,29
4	Балкон	7,44
		38,65 м²

Примечания:

Обязательно перепроверить размеры помещения, тк могут быть расхождения с обмерным планом!!!

- 1) Все размеры указаны без учета отделочных материалов.
- 2) Уточнить какой замок при входе в номер, и где размещать.
- 3)Обмерный план выполнен по обмерам сторонней организации и может не учитывать все особенности помещения и иметь размеры, отличающиеся от реальных.
- 4) Перед началом строительных работ все размеры необходимо уточнить на месте.
- 5) Утвердить открывание дверей.
- 6) Все уточнения, изменения по проекту согласовывать с заказчиком и дизайнером.

Условные обозначения:

- зона прихожей
- зона гостиной
- санузел
- балкон

Изм.	Коп.уч.	Лист	№Док.	Подп.	Дата				
						Room 481	Стадия	Лист	Листов
						План расстановки мебели. М1:70			