
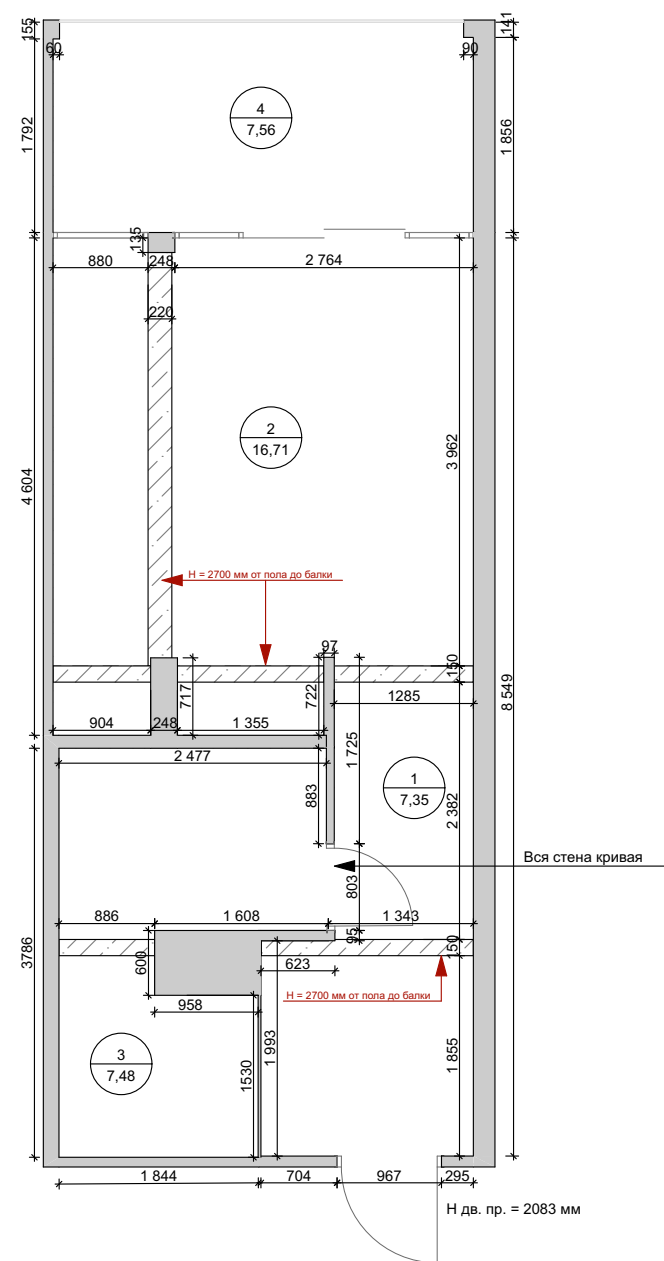


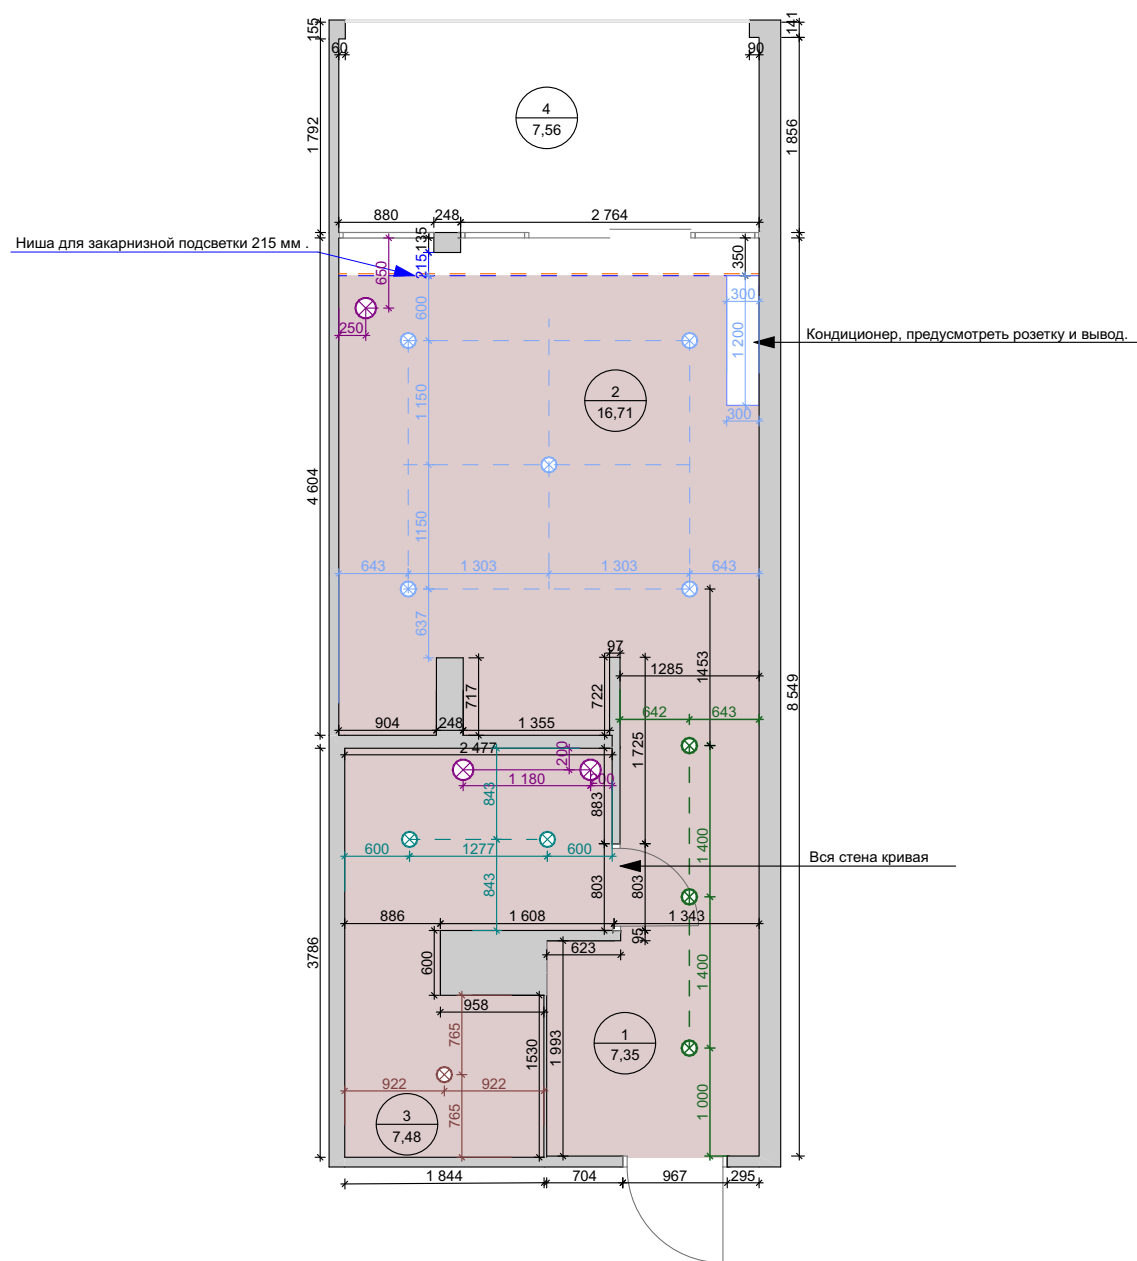

№	Наименование	Площадь
1	Прихожая	7,35
2	Зона спальни	16,71
3	Санузел	7,48
4	Балкон	7,56
		39,10 м²

Примечания:

- 1) Уточнить размещение кондиционеров, их управление (с пульта, или панель на стене).
- 2) Уточнить открывание дверей.
- 3) Обмерный план выполнен по обмерам сторонней организации и может не учитывать все особенности помещения и иметь размеры, отличающиеся от реальных.
- 4) Перед началом строительных работ все размеры необходимо уточнить на месте.
- 5) Все размеры указаны без учета отделочных материалов.

Условные обозначения:

-  - балка
-  - влагостойкий натяжной потолок.
-  - подвесной светильник в санузле - 2 шт
-  - подвесной светильник в зоне спальни у кровати - 1 шт
-  - встроенный потолочный светильник в зоне спальни - 5 шт
-  - встроенный потолочный светильник в прихожей - 3 шт
-  - встроенный потолочный светильник в санузле - 2 шт
-  - встроенный потолочный светильник в санузле в душевой- 1 шт
-  - светодиодная лента

Изм.	Копуч.	Лист	№Док.	Подп.	Дата					
						Room 482		Стадия	Лист	Листов
						План потолка. М1:70				