


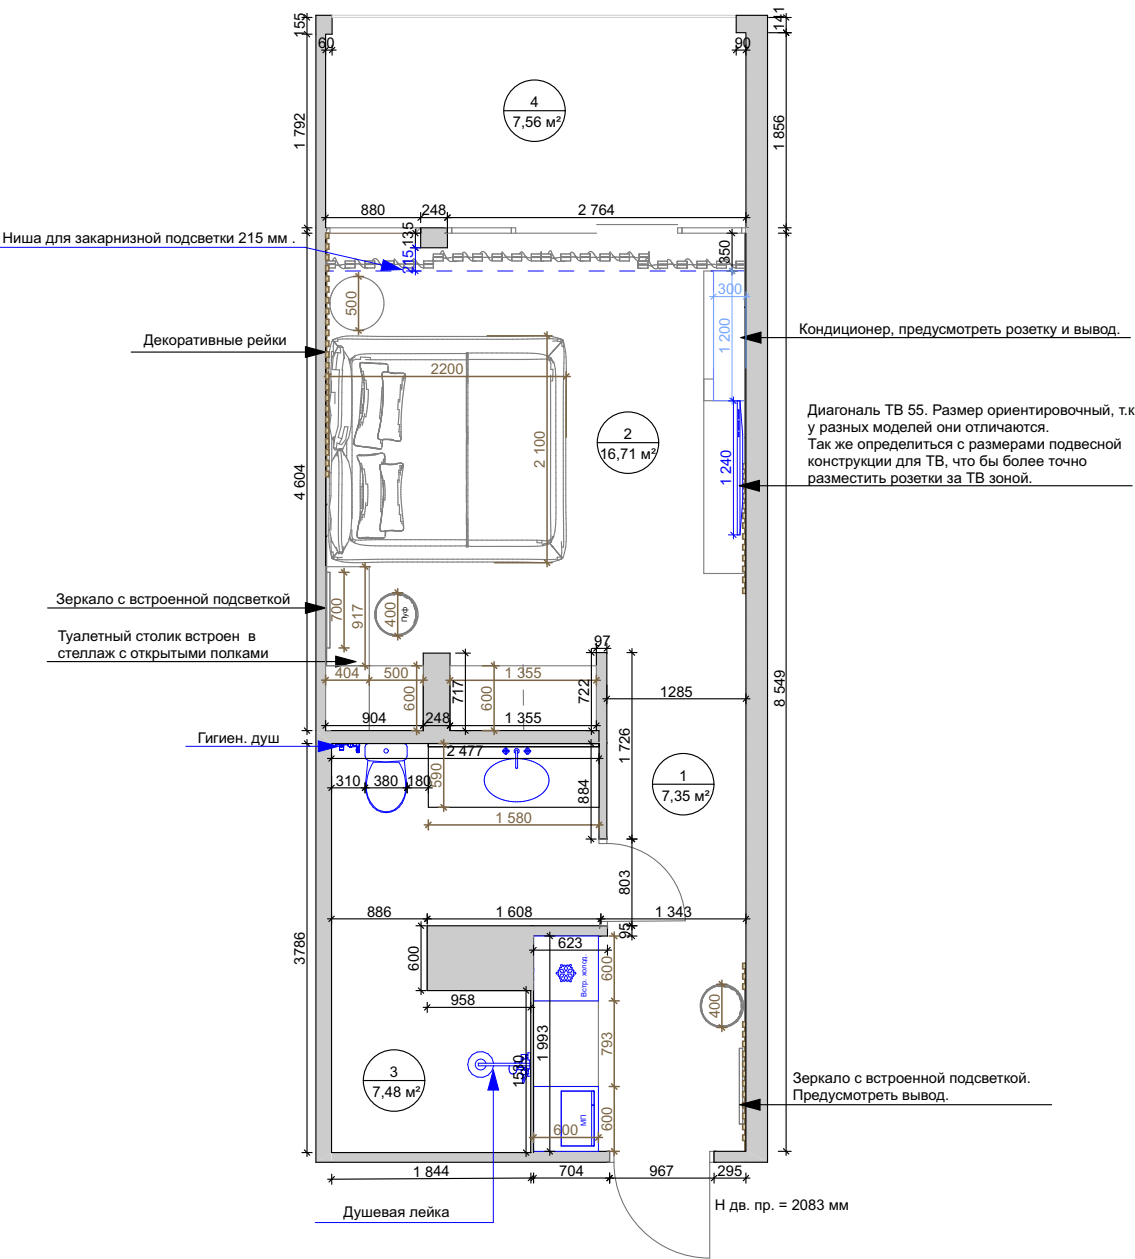

№	Наименование	Площадь
1	Прихожая	7,35
2	Зона спальни	16,71
3	Санузел	7,48
4	Балкон	7,56
		39,10 м²

Обязательно перепроверить размеры помещения, тк могут быть расхождения с обмерным планом!!!

- 1)Уточнить размещение кондиционеров, их управление (с пульта, или панель на стене).
- 2) Уточнить какой замок при входе в номер, и где размещать.
- 3)Обмерный план выполнен сторонней организацией и может не учитывать все особенности помещения и иметь размеры, отличающиеся от реальных.
- 4) Перед началом строительных работ все размеры необходимо уточнить на месте.
- 5) Все размеры указаны без учета отделочных материалов.
- 6) Сантехническое оборудование в санузле находится на прежних местах, что бы не демонтировать плитку и сантехническое оборудование.

Изм.	Копуч.	Лист	№Док.	Подп.	Дата	Room 482	Стадия	Лист	Листов
						План размещения сантехнического и электрооборудования. М1:70			