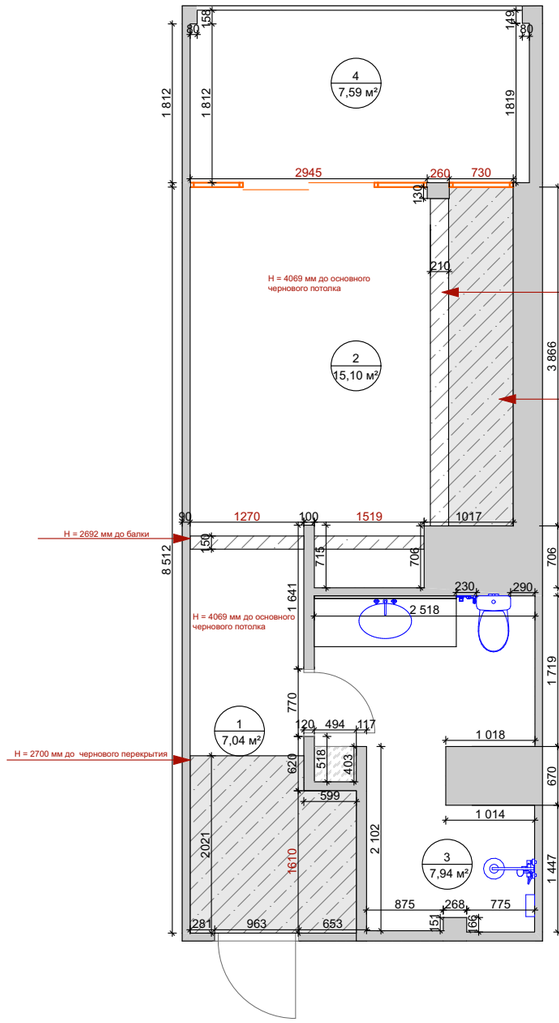

Кондиционер 150 мм мин. расстояние от потолка до размещения кондиционера. Предусмотреть розетку и вывод. Размеры кондиционера условные. Точные размеры будут определены после утверждения модели

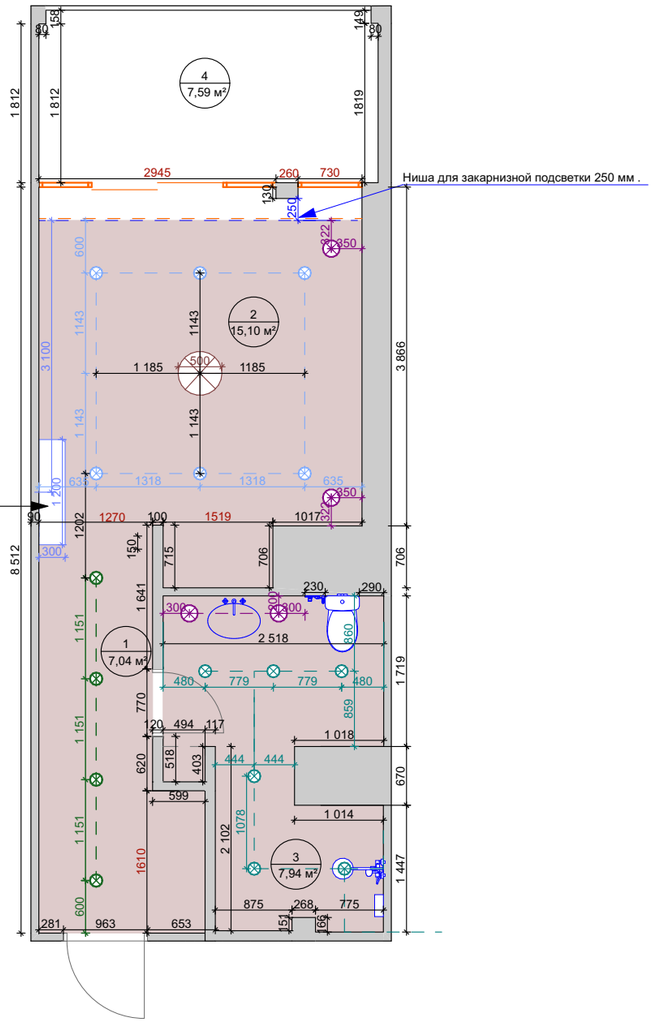

№	Наименование	Площадь
1	Прихожая	7,04
2	Зона спальни	15,10
3	Санузел	7,94
4	Балкон	7,59
		37,67 м²

Примечания:

Обязательно перепроверить размеры помещения, тк могут быть расхождения с обмерным планом!!!

1)Уточнить размещение кондиционеров, их управление (с пульта, или панель на стене).
2) Уточнить какой замок при входе в номер, и где размещать.
3)Обмерный план выполнен по обмерам заказчика и может не учитывать все особенности помещения и иметь размеры, отличающиеся от реальных.
4) Перед началом строительных работ все размеры необходимо уточнить на месте.
5) Все выключатели и розетки в санузле влагостойкие.
6) Все отверстия в санузле для электрики (розетки, выключатели) остаются на прежних местах, что бы не демонтировать плитку.
7) Уточнить размеры профиля для светодиодной ленты для зеркал, и профиля для подсветки кухонной зоны.
8) Уточнить размеры настенных декоративных реек.

Условные обозначения:

- черновое перекрытие
- балка
- влагостойкий натяжной потолок. Зона прихожей и спальни 20,73 м², санузел 7,84 м²
- потолочный светильник с встроенным вентилятором - 1 шт
- подвесной светильник в спальне - 2 шт
- подвесной светильник в санузле - 2 шт
- встроенный потолочный светильник в зоне спальни - 6 шт
- встроенный потолочный светильник в прихожей - 4 шт
- встроенный потолочный светильник в санузле - 6 шт

Изм.	Кол.уч.	Лист	№Док.	Подп.	Дата			
						Room 484	Стадия	Лист	Листов
						План потолка. М1:70			