


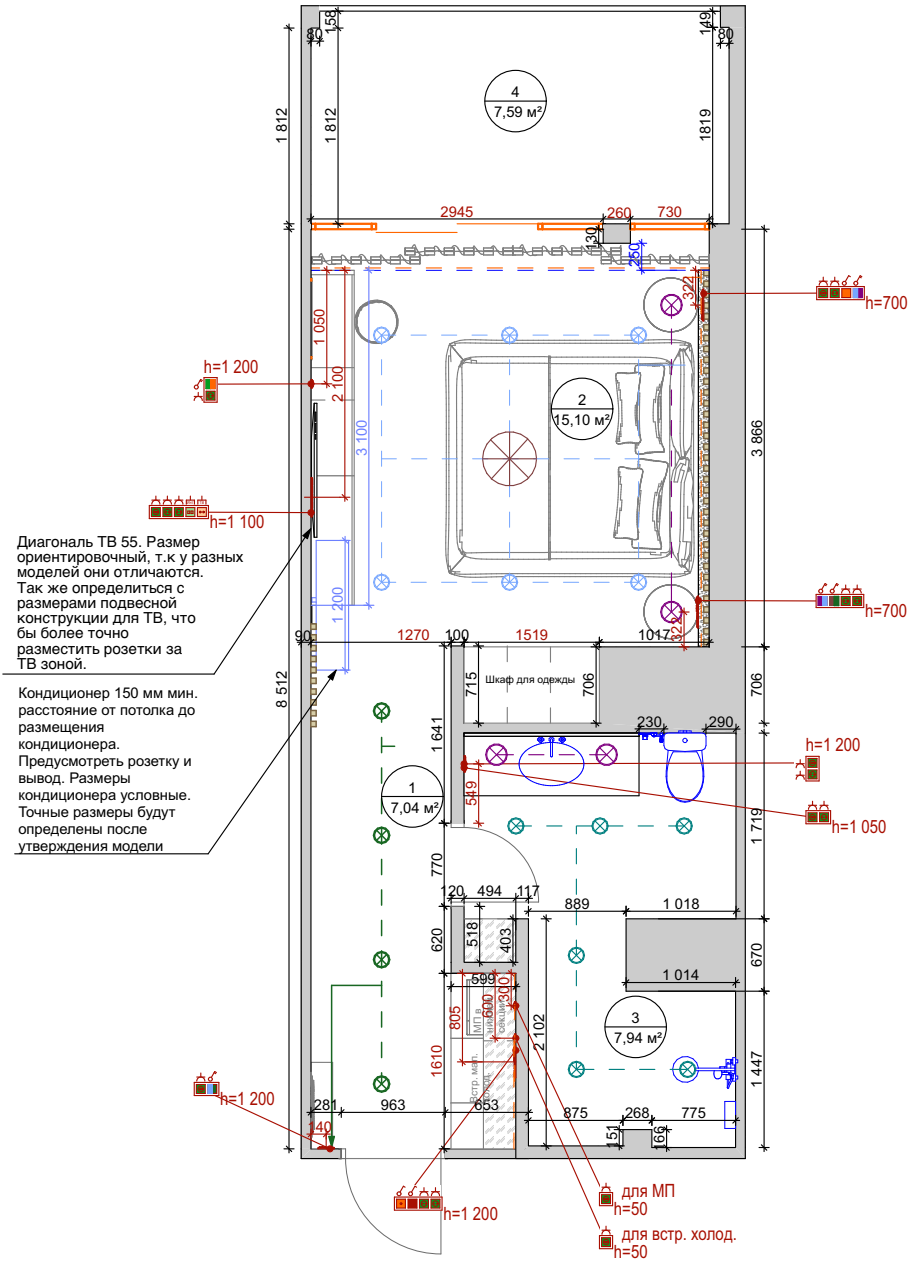

№	Наименование	Площадь
1	Прихожая	7,04
2	Зона спальни	15,10
3	Санузел	7,94
4	Балкон	7,59
		37,67 м²

Примечания:

Обязательно перепроверить размеры помещения, тк могут быть расхождения с обмерным планом!!!

- 1)Уточнить размещение кондиционеров, их управление (с пульта, или панель на стене).
- 2) Уточнить какой замок при входе в номер, и где размещать.
- 3)Обмерный план выполнен по обмерам заказчика и может не учитывать все особенности помещения и иметь размеры, отличающиеся от реальных.
- 4) Перед началом строительных работ все размеры необходимо уточнить на месте.
- 5) Все выключатели и розетки в санузеле влагостойкие.
- 6) Все отверстия в санузеле для электрики (розетки, выключатели) остаются на прежних местах, что бы не демонтировать плитку.
- 7) Уточнить размеры профиля для светодиодной ленты для зеркал, и профиля для подсветки кухонной зоны.
- 8) Уточнить размеры настенных декоративных реек.

Изм.	Копуч.	Лист	№Док.	Подп.	Дата				
						Room 484	Стадия	Лист	Листов
						План размещения розеток. М1:70			