


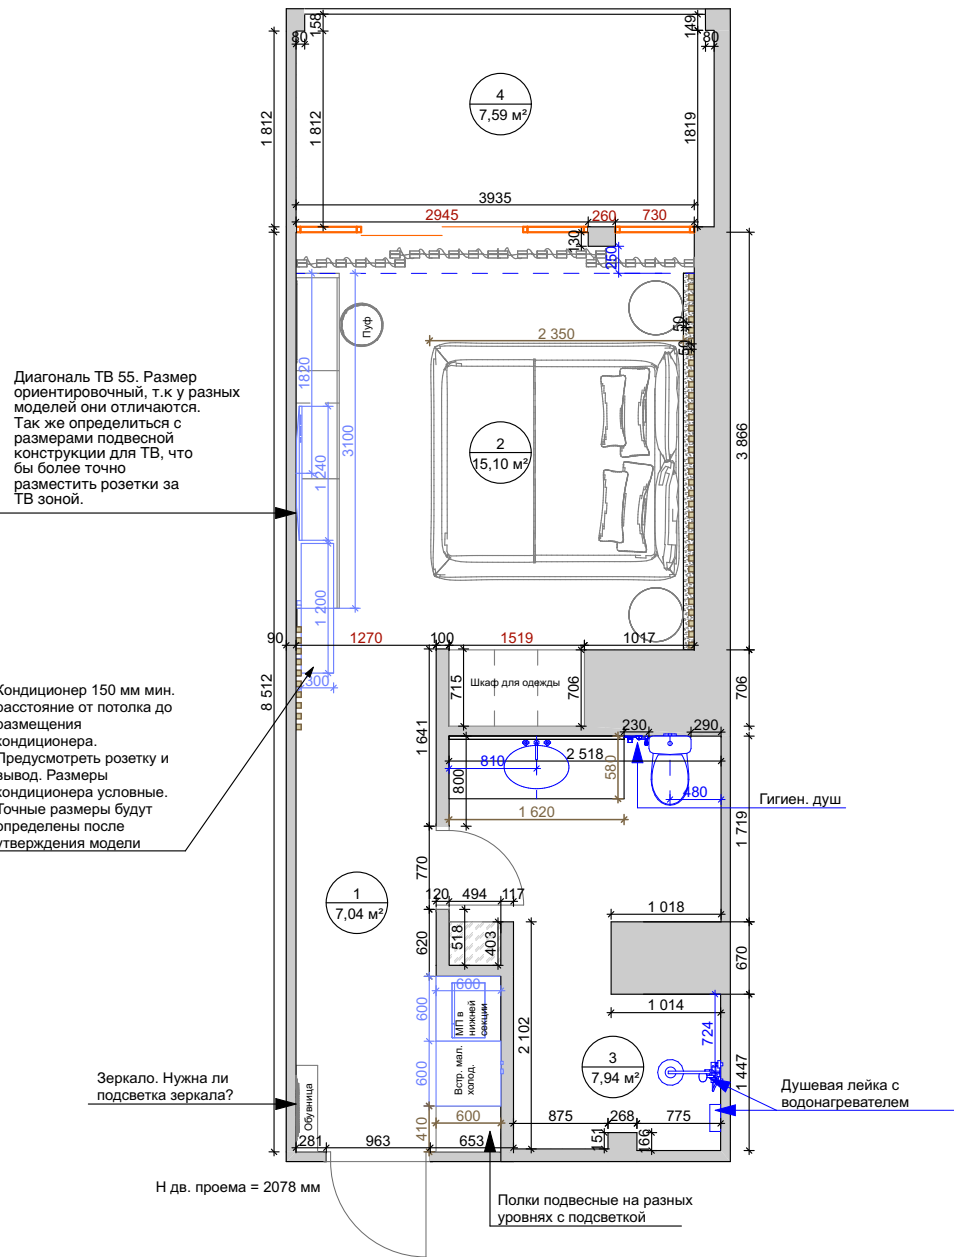

№	Наименование	Площадь
1	Прихожая	7,04
2	Зона спальни	15,10
3	Санузел	7,94
4	Балкон	7,59
		37,67 м²

Примечания:

Обязательно перепроверить размеры помещения, тк могут быть расхождения с обмерным планом!!!

- 1) Уточнить размещение кондиционеров, их управление (с пульта, или панель на стене).
2) Сантехническое оборудование в санузле находится на прежних местах, что бы не демонтировать плитку и сантехническое оборудование.
3) Обмерный план выполнен по обмерам заказчика и может не учитывать все особенности помещения и иметь размеры, отличающиеся от реальных.
4) Перед началом строительных работ все размеры необходимо уточнить на месте.

Изм.	Копуч.	Лист	№Док.	Подп.	Дата				
						Room 484	Стадия	Лист	Листов
						План расстановки размещения сантехнического и электрооборудования . М1:70			