


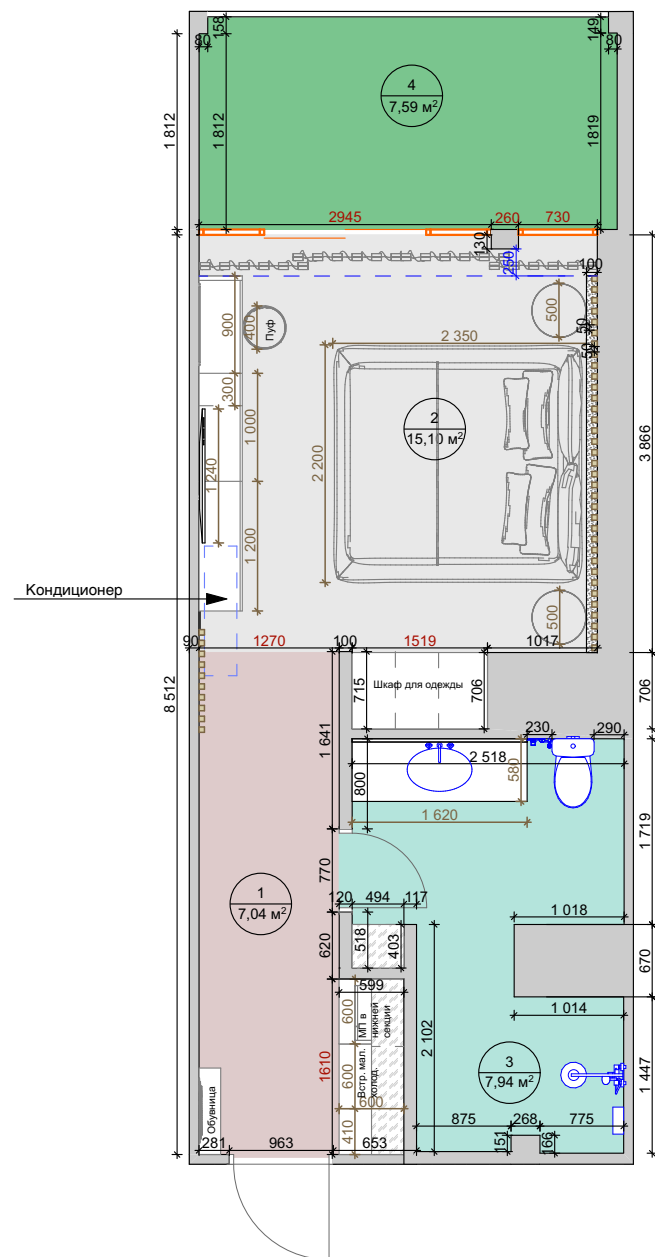

Примечания:

Обязательно перепроверить размеры помещения, тк могут быть расхождения с обмерным планом!!!

- 1) Уточнить размещение кондиционеров, их управление (с пульта, или панель на стене).
- 2) Уточнить открывание дверей.
- 3) Уточнить какой замок при входе в номер, и где размещать.
- 4) Обмерный план выполнен по обмерам заказчика и может не учитывать все особенности помещения и иметь размеры, отличающиеся от реальных.
- 5) Перед началом строительных работ все размеры необходимо уточнить на месте.
- 6) Уточнить размеры профиля для светодиодной ленты для зеркал, и профиля для подсветки кухонной зоны.
- 7) Уточнить размеры настенных декоративных реек.

- зона прихожей
- зона спальни
- санузел
- балкон

Изм.	Копуч.	Лист	№Док.	Подп.	Дата					
						Room 484		Стадия	Лист	Листов
						План расстановки мебели. М1:70				