




Развертка 1

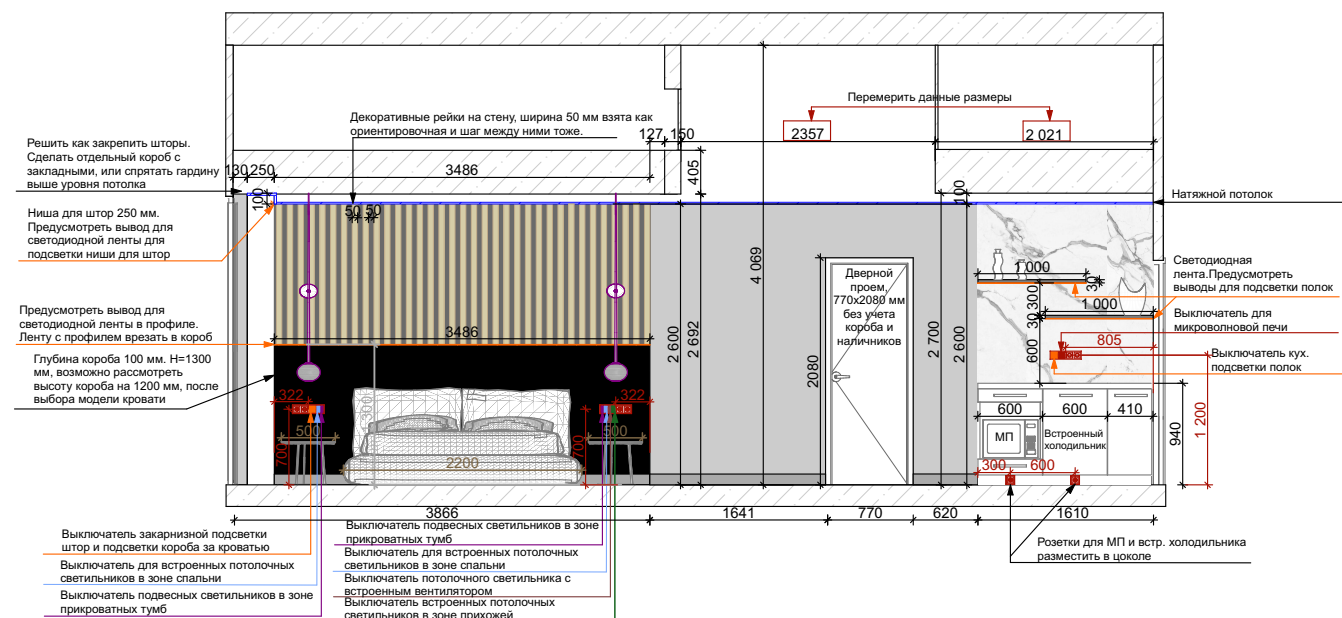


Развертка 2

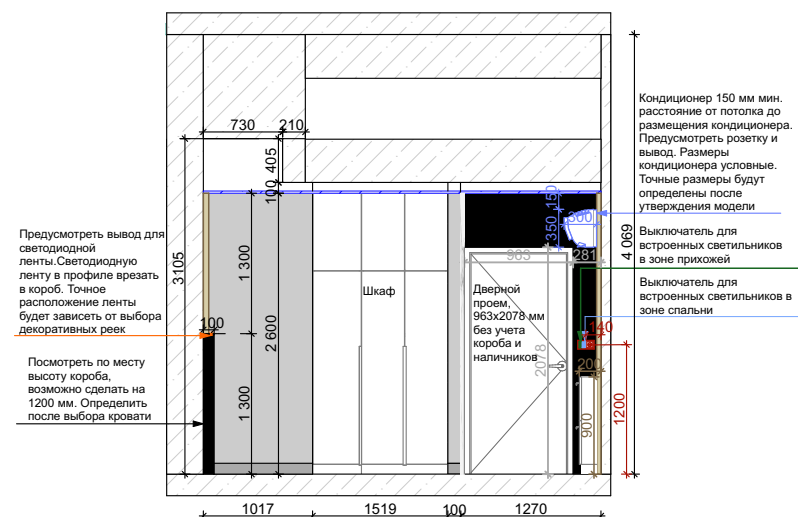


Развертка 3

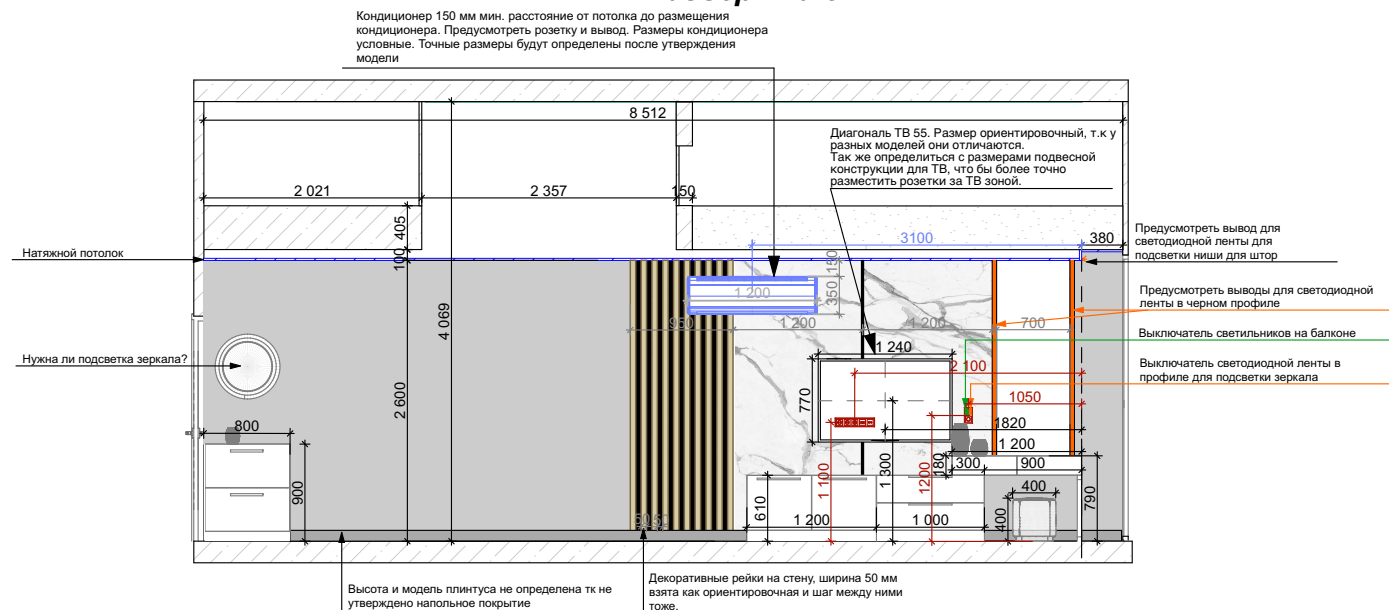

Развертка 4

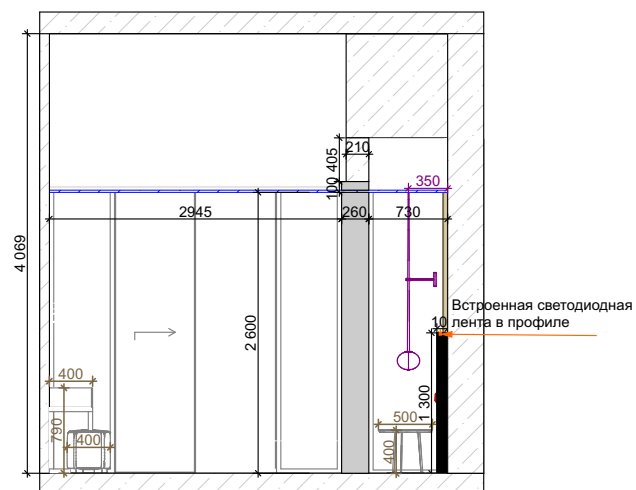

№	Наименование	Площадь
1	Прихожая	7,04
2	Зона спальни	15,10
3	Санузел	7,94
4	Балкон	7,59
		37,67 м²

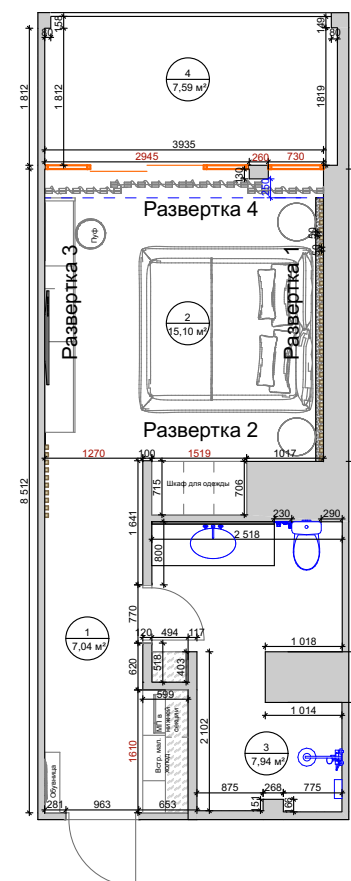

Изм.	Копуч.	Лист	№Док.	Подп.	Дата					
						Room 484		Стадия	Лист	Листов
						Развертки. М1:70				