


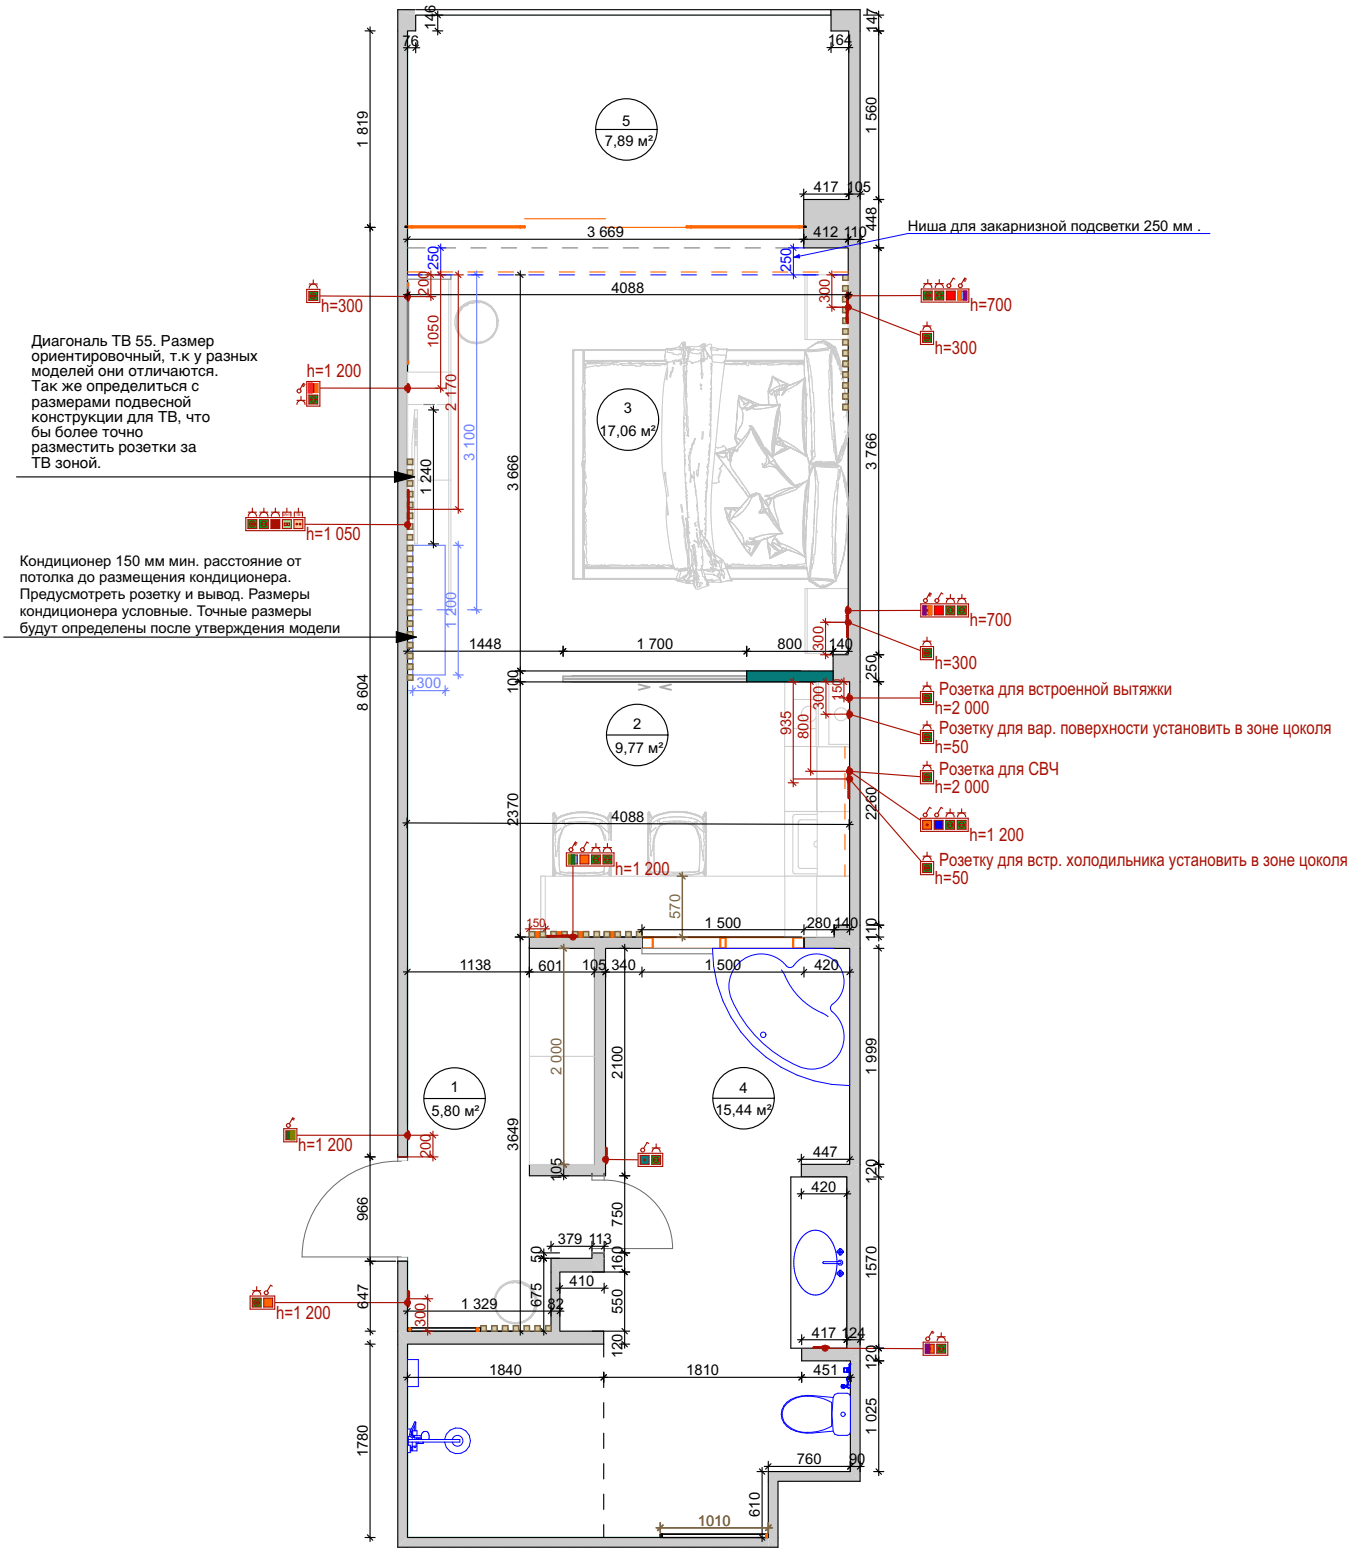

№	Наименование	Площадь
1	Прихожая	5,80
2	Зона кухни	9,77
3	Зона спальни	17,06
4	Санузел	15,44
5	Балкон	7,89
		55,96 м²

Примечания:

- 1)Диагональ ТВ 55. Размер ориентировочный, т.к у разных моделей они отличаются.
- 2)Так же определиться с размерами подвесной конструкции для ТВ, что бы более точно разместить розетки за ТВ зоной.
- 3)Определиться с системой карточек в номер при входе, на какой высоте они будут размещены.
- 4)Определиться с моделью кондиционера и его управлением.
- 5)Розетки за прикроватными тумбами на Н=300 мм установлены на случай если будут прикроватные тумбы с встроенной зарядкой и подсветкой.
- 6) Все розетки и выключатели в санузле установить в уже существующих местах.

Изм.	Копуч.	Лист	№Док.	Подп.	Дата	Room 485	Стадия	Лист	Листов
						План размещения розеток и выключателей. М1:70			