

Развертка 1

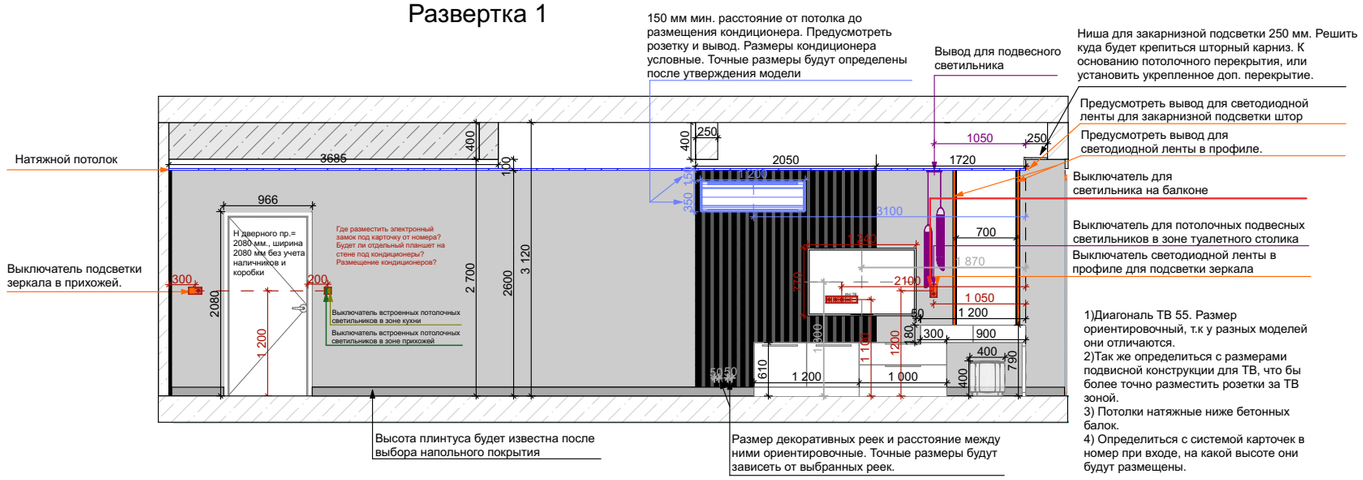


1)Диагональ ТВ 55. Размер ориентировочный, т.к у разных моделей они отличаются.
2)Так же определиться с размерами подвисной конструкции для ТВ, что бы более точно разместить розетки за ТВ зоной.
3) Потолки натяжные ниже бетонных балок.
4) Определиться с системой карточек в номер при входе, на какой высоте они будут размещены.


Развертка 2

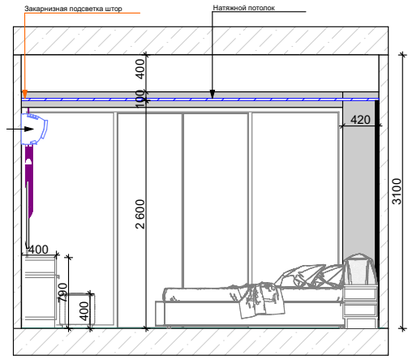


Развертка 3

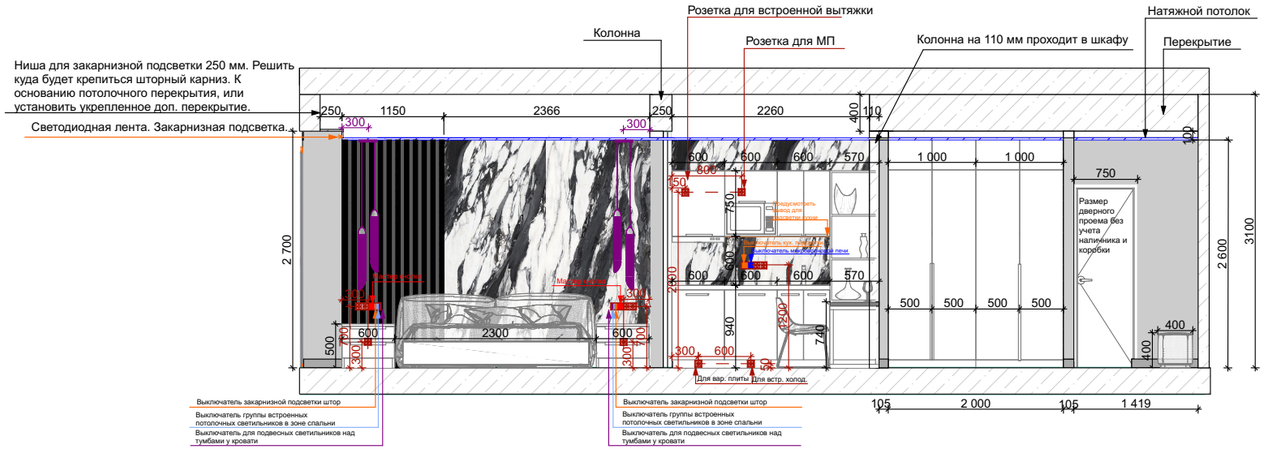


Развертка 4

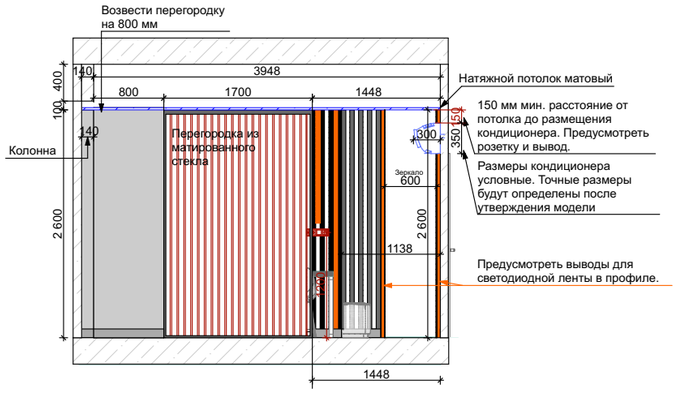

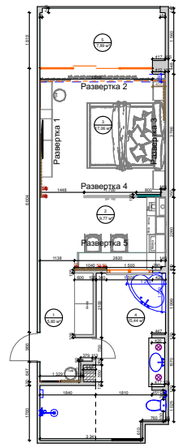

Развертка 5

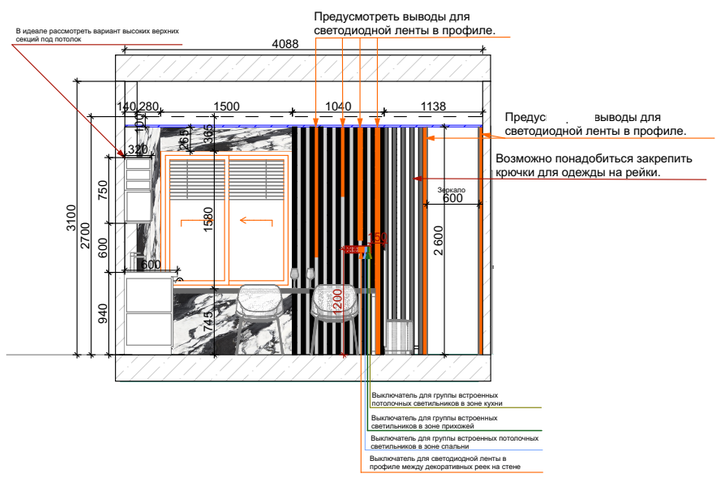

Изм.	Кол.уч.	Лист	№Док.	Подп.	Дата				
						Room 485	Стадия	Лист	Листов
						Развертки. М1:70			